



## Woonzorgcentrum Nieuwehagen

Woonzorgcentrum met 31 appartementen te 's-Hertogenbosch

Datum: 04 - 12 - 2006

CARTOTHEEK

# Inhoud Cartotheek

1	Situatie	1 : 500	21	Appartement 1 Buitenkozijnen	1 : 50
2a	Plattegrond Kelder	1 : 300	22	Appartement 2 Buitenkozijnen	1 : 50
2b	Plattegrond Begane Grond	1 : 300	23	Appartement 3a Buitenkozijnen	1 : 50
2c	Plattegrond 1e Verdieping	1 : 300	24	Appartement 3 Buitenkozijnen	1 : 50
2d	Plattegrond 2e Verdieping	1 : 300	25	Appartement 4 Buitenkozijnen	1 : 50
2e	Plattegrond 3e Verdieping	1 : 300	26	Appartement 5 Buitenkozijnen	1 : 50
2	Plattegrond 4e verdieping	1 : 200	27	Appartement 6 Buitenkozijnen	1 : 50
3	Plattegrond 5e verdieping	1 : 200	28	Appartement 7 Buitenkozijnen	1 : 50
4	Plattegrond 6e verdieping	1 : 200	29	Appartement 8 Buitenkozijnen	1 : 50
5	Plattegrond 7e verdieping	1 : 200	30	Appartement 1 Binnenkozijnen	1 : 50
6	Gevelaanzicht noordoost	1 : 200	31	Appartement 2 Binnenkozijnen	1 : 50
7	Gevelaanzicht noordwest	1 : 200	32	Appartement 3a Binnenkozijnen	1 : 50
8	Gevelaanzicht zuidwest	1 : 200	33	Appartement 3 Binnenkozijnen	1 : 50
9	Gevelaanzicht zuidoost	1 : 200	34	Appartement 4 Binnenkozijnen	1 : 50
10	Doorsnede A - A	1 : 200	35	Appartement 5 Binnenkozijnen	1 : 50
11	Doorsneden B - B	1 : 200	36	Appartement 6 Binnenkozijnen	1 : 50
12	Plattegrond Type 1	1 : 50	37	Appartement 7 Binnenkozijnen	1 : 50
13	Plattegrond Type 2	1 : 50	38	Appartement 8 Binnenkozijnen	1 : 50
14	Plattegrond Type 3a	1 : 50	39	Binnenkozijnen hal	1 : 50
15	Plattegrond Type 3	1 : 50			
16	Plattegrond Type 4	1 : 50			
17	Plattegrond Type 5	1 : 50			
18	Plattegrond Type 6	1 : 50			
19	Plattegrond Type 7	1 : 50			
20	Plattegrond Type 8	1 : 50			


BrabantWonen  
Postbus 151  
5340AD OSS  
info@brabantwonen.nl

Wooncomplex Nieuwehagen

Woonzorgcentrum met 31 appartementen

Inhoud Cartotheek		Tek.no.:	0
Schaal:	-		
Formaat:	A3		
Get.:	rnka		
Gew.:	dec 2006		



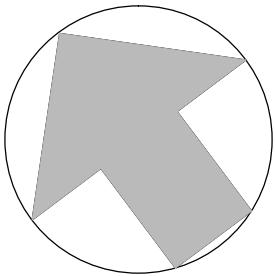

# RIVIER DE A A

BrabantWonen  
Postbus 151  
5340AD OSS  
info@brabantwonen.nl


## Wooncomplex Nieuwehagen

Woonzorgcentrum met 31 appartementen

### Situatie

Tek.no.: 1


Schaal:	1 a 500
Formaat:	A3
Get.:	mka
Gew.:	dec 2006

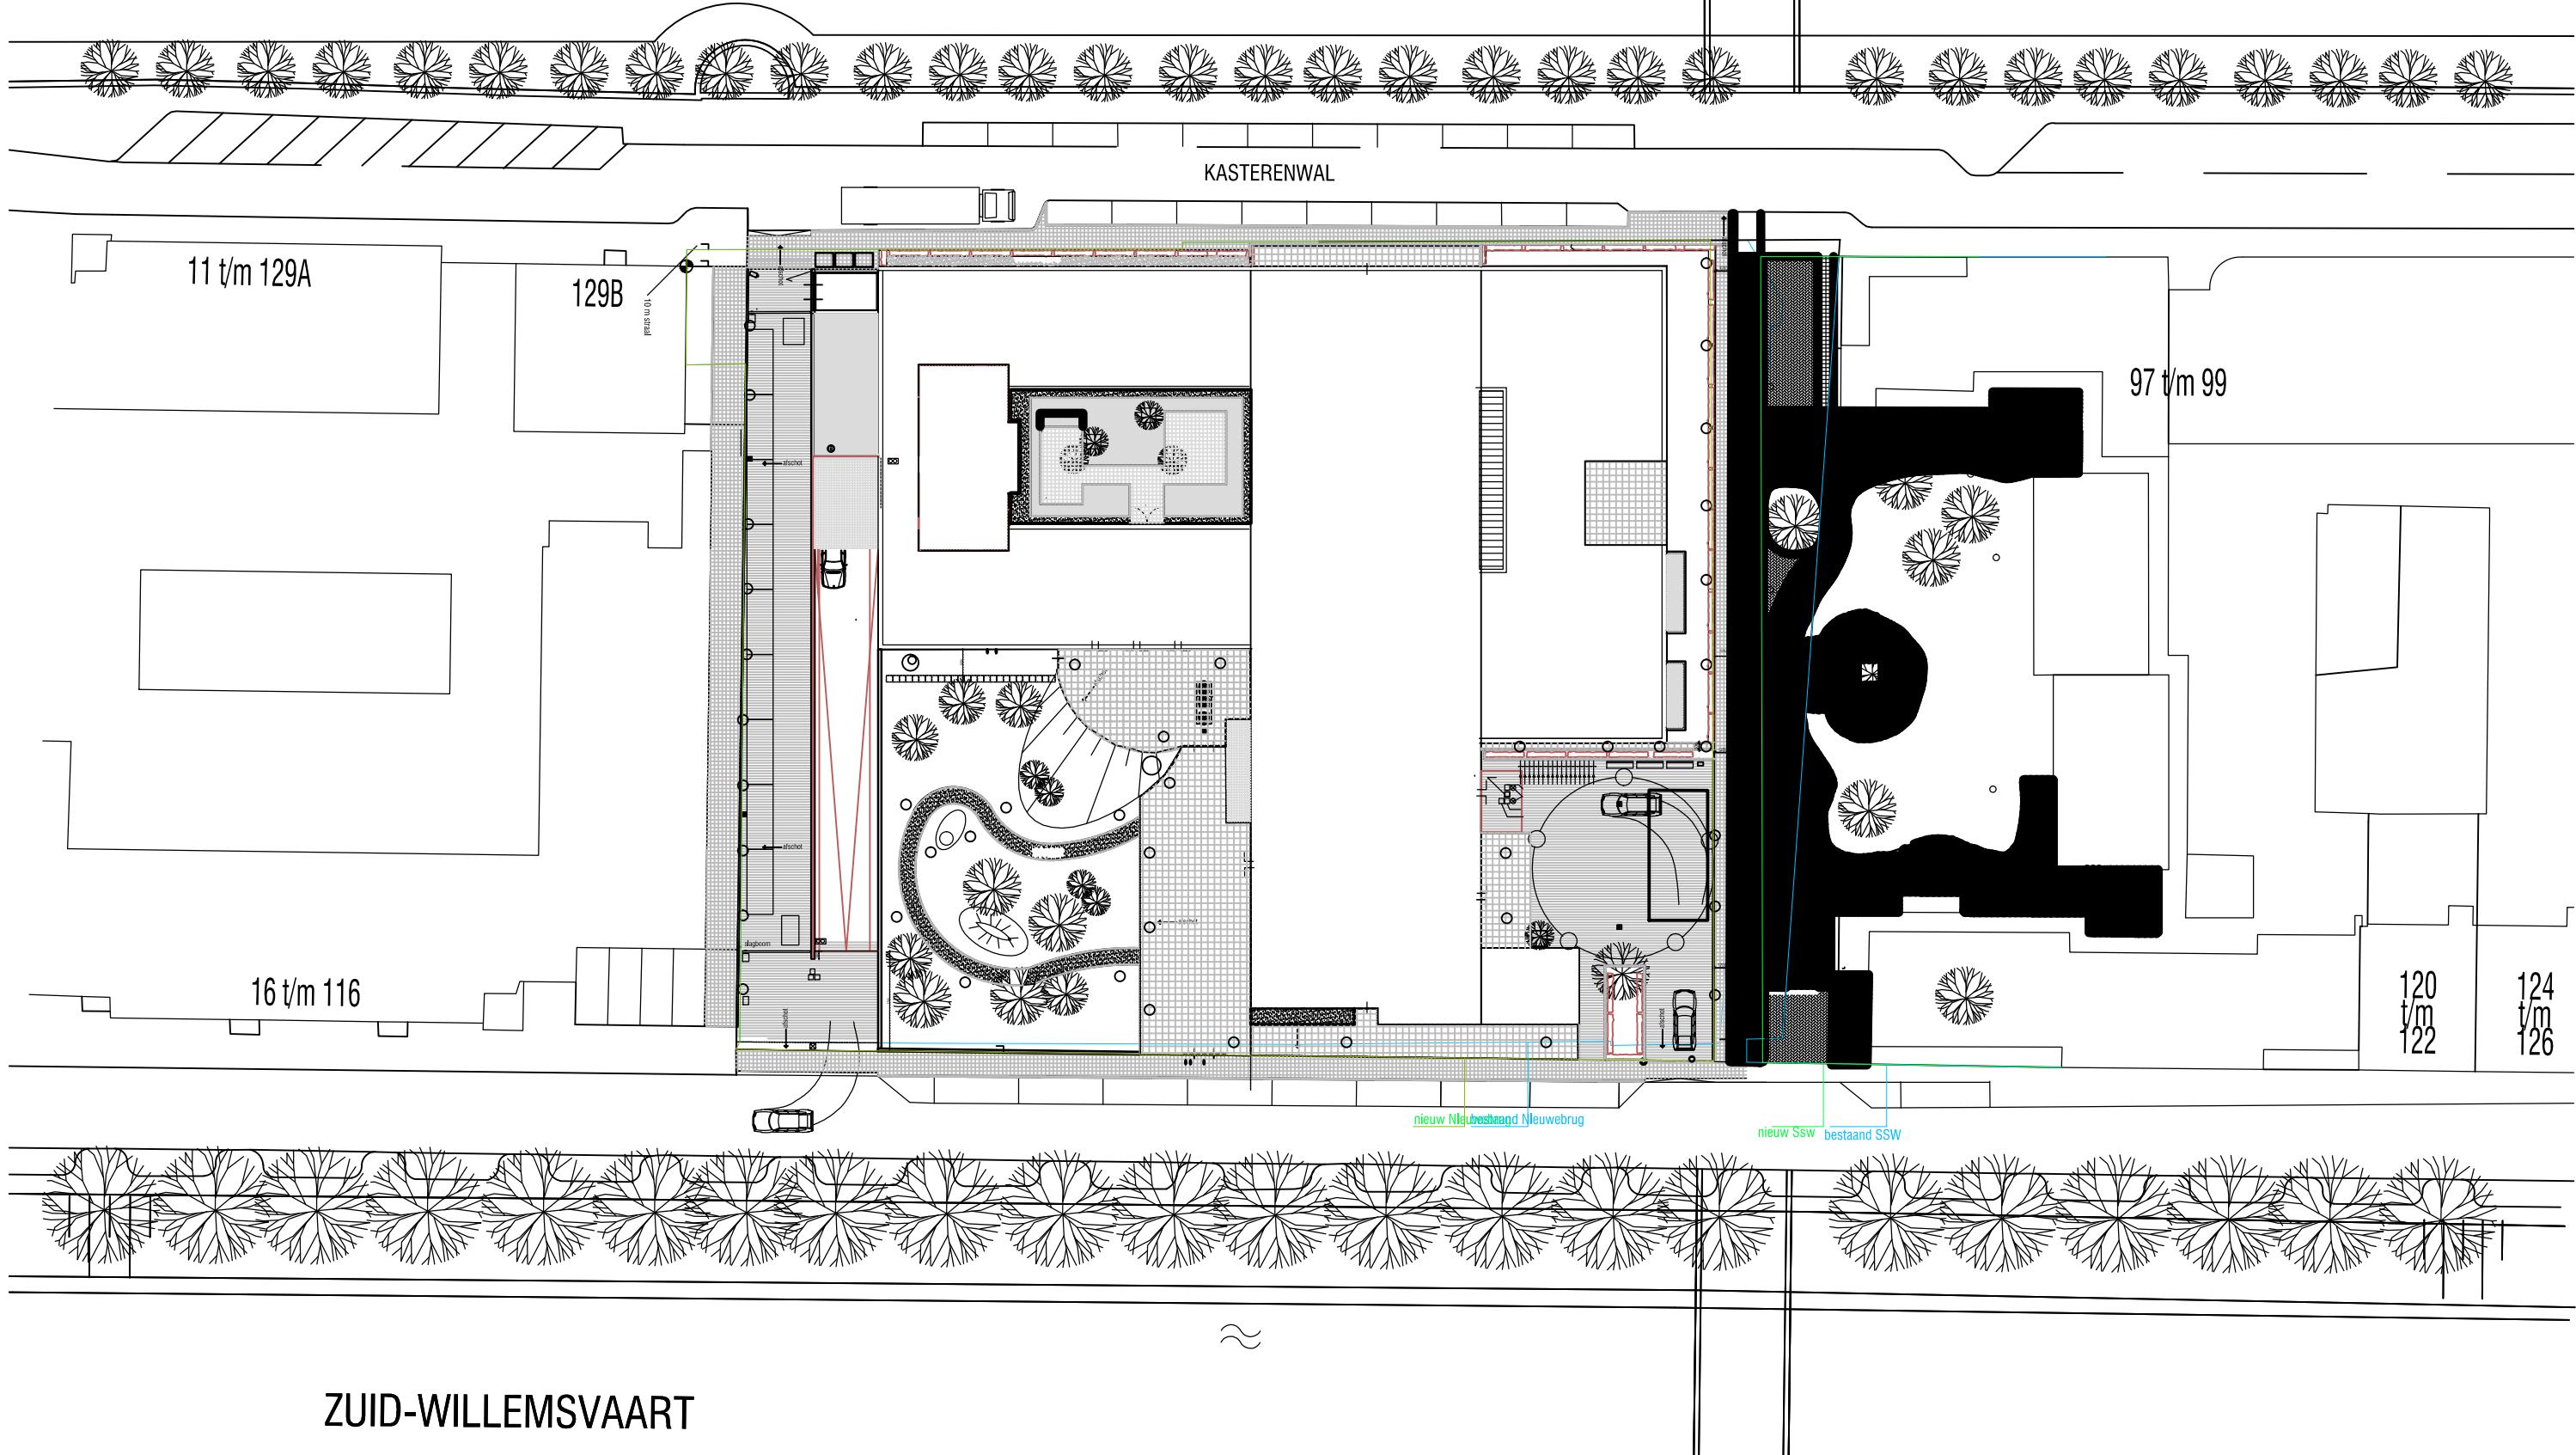

Plattegrond Kelder

Tek.no.: 2a

Schaal:	1 a 300
Formaat:	A3
Get.:	mka
Gew.:	dec 2006

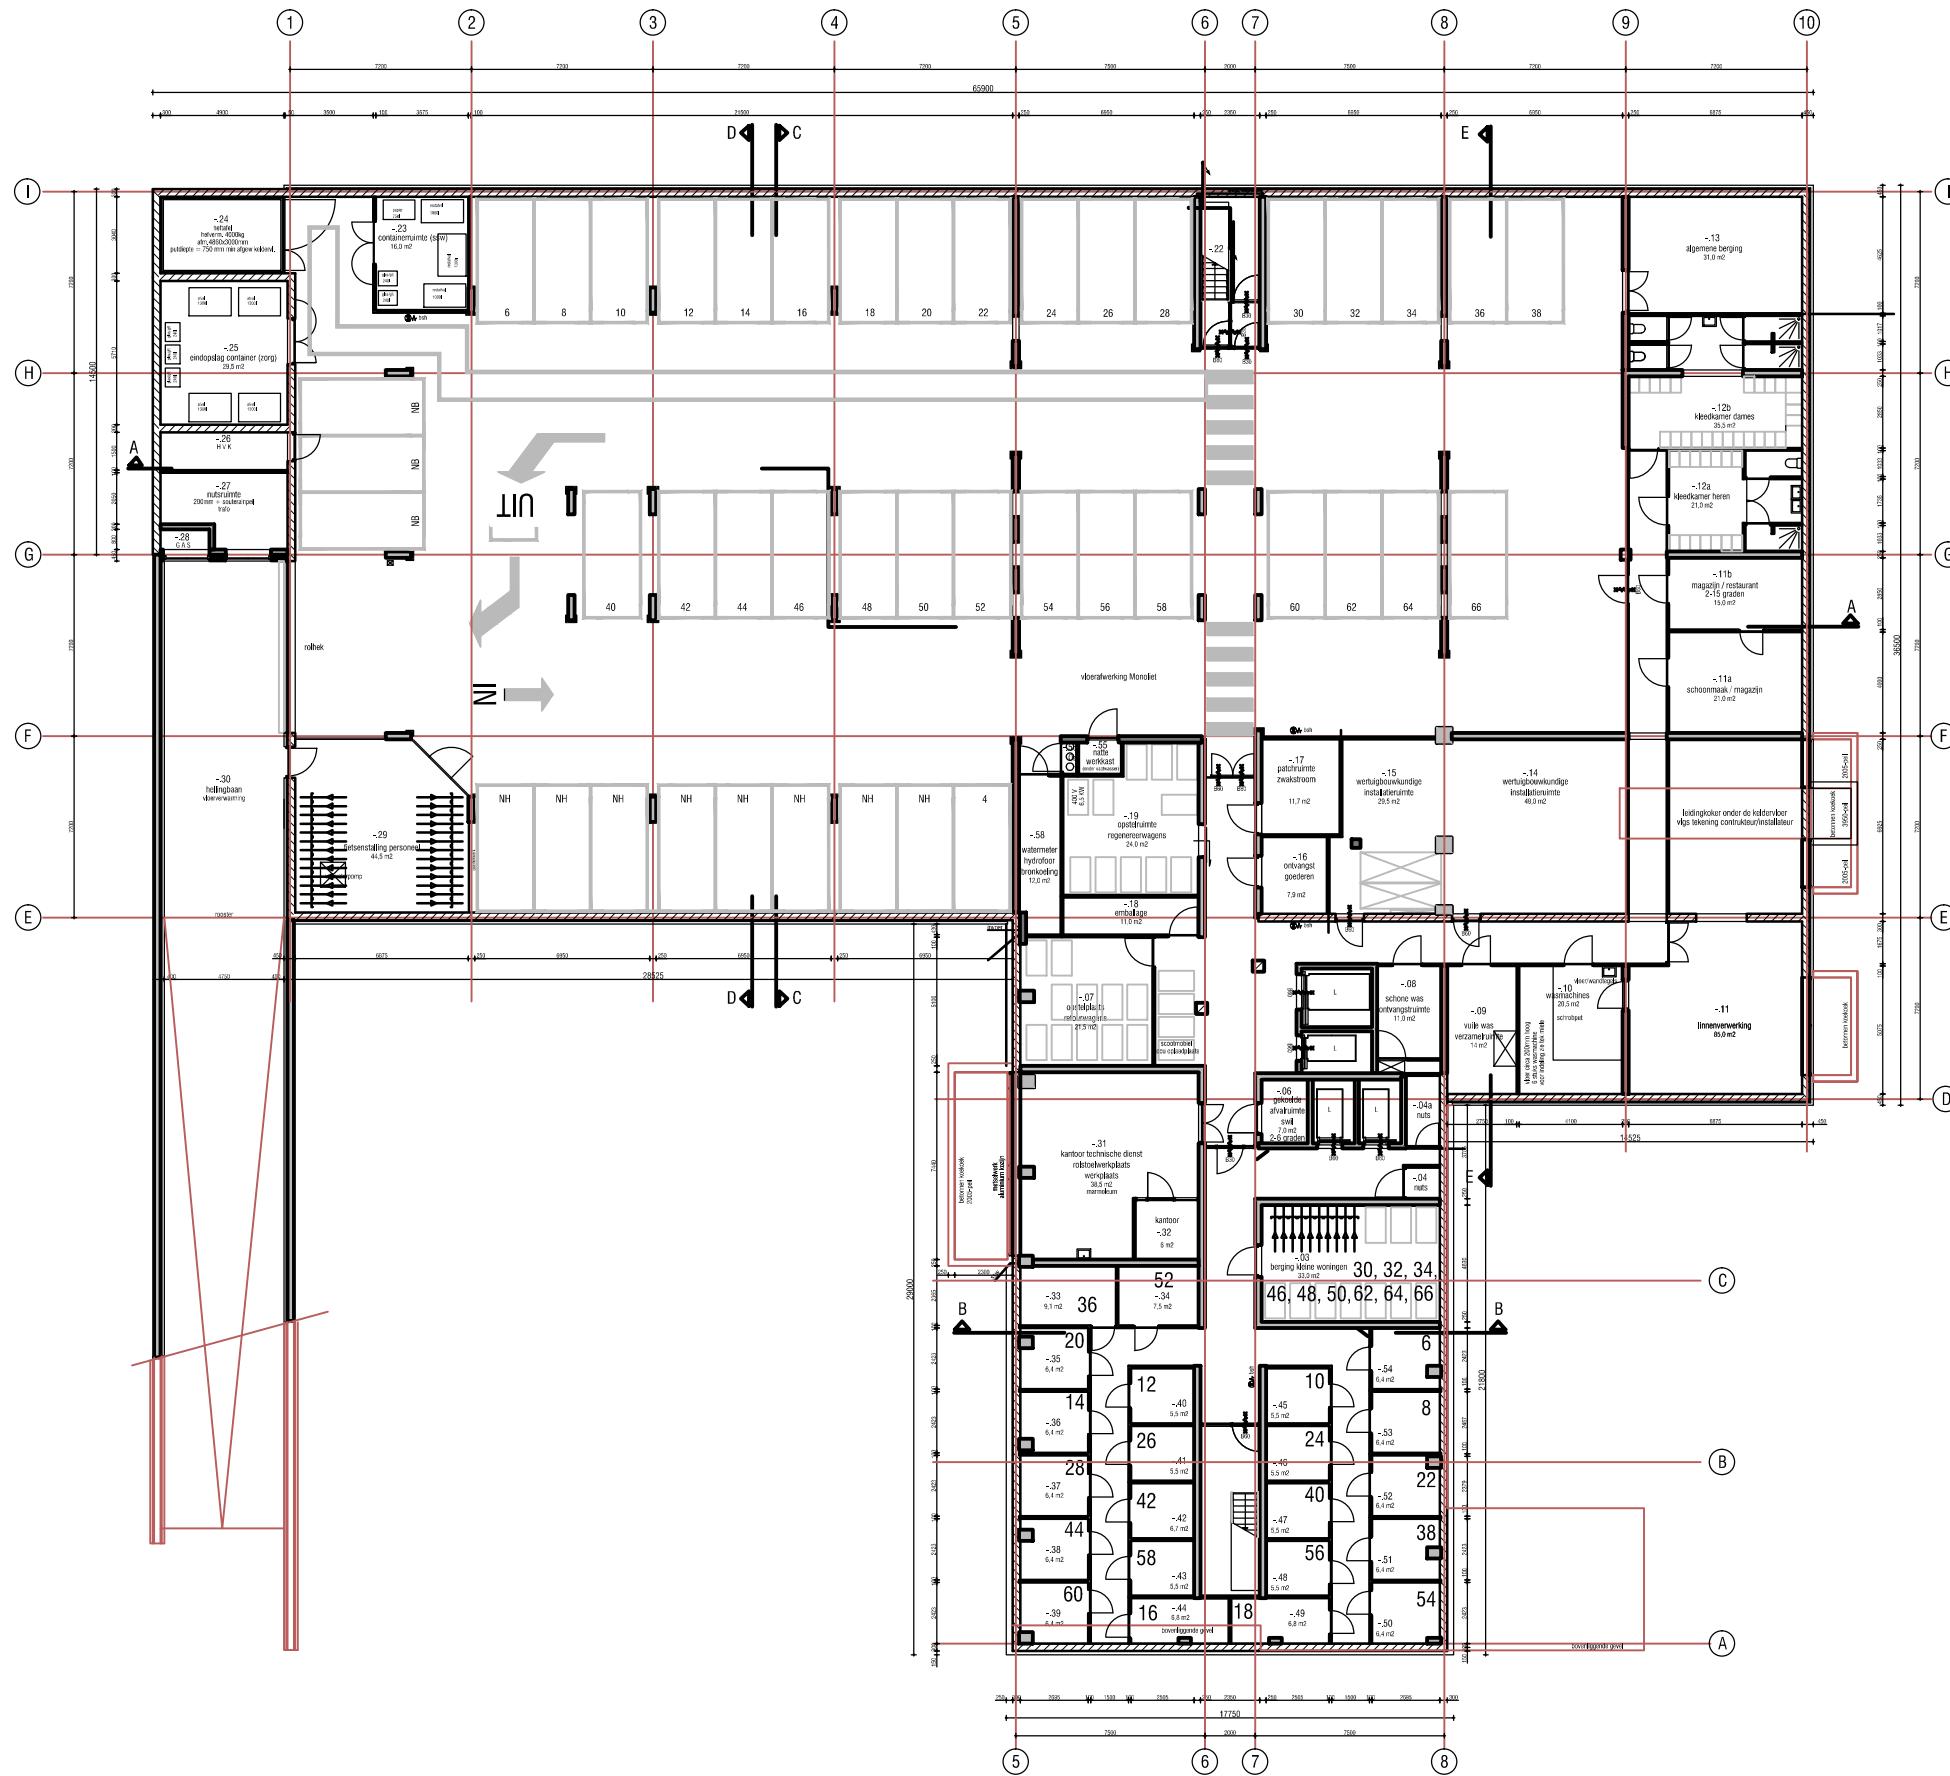

BrabantWonen  
Postbus 151  
5340AD OSS  
info@brabantwonen.nl


## Wooncomplex Nieuwehagen

Woonzorgcentrum met 31 appartementen

### Plattegrond Begane Grond

ek.no.:


2b

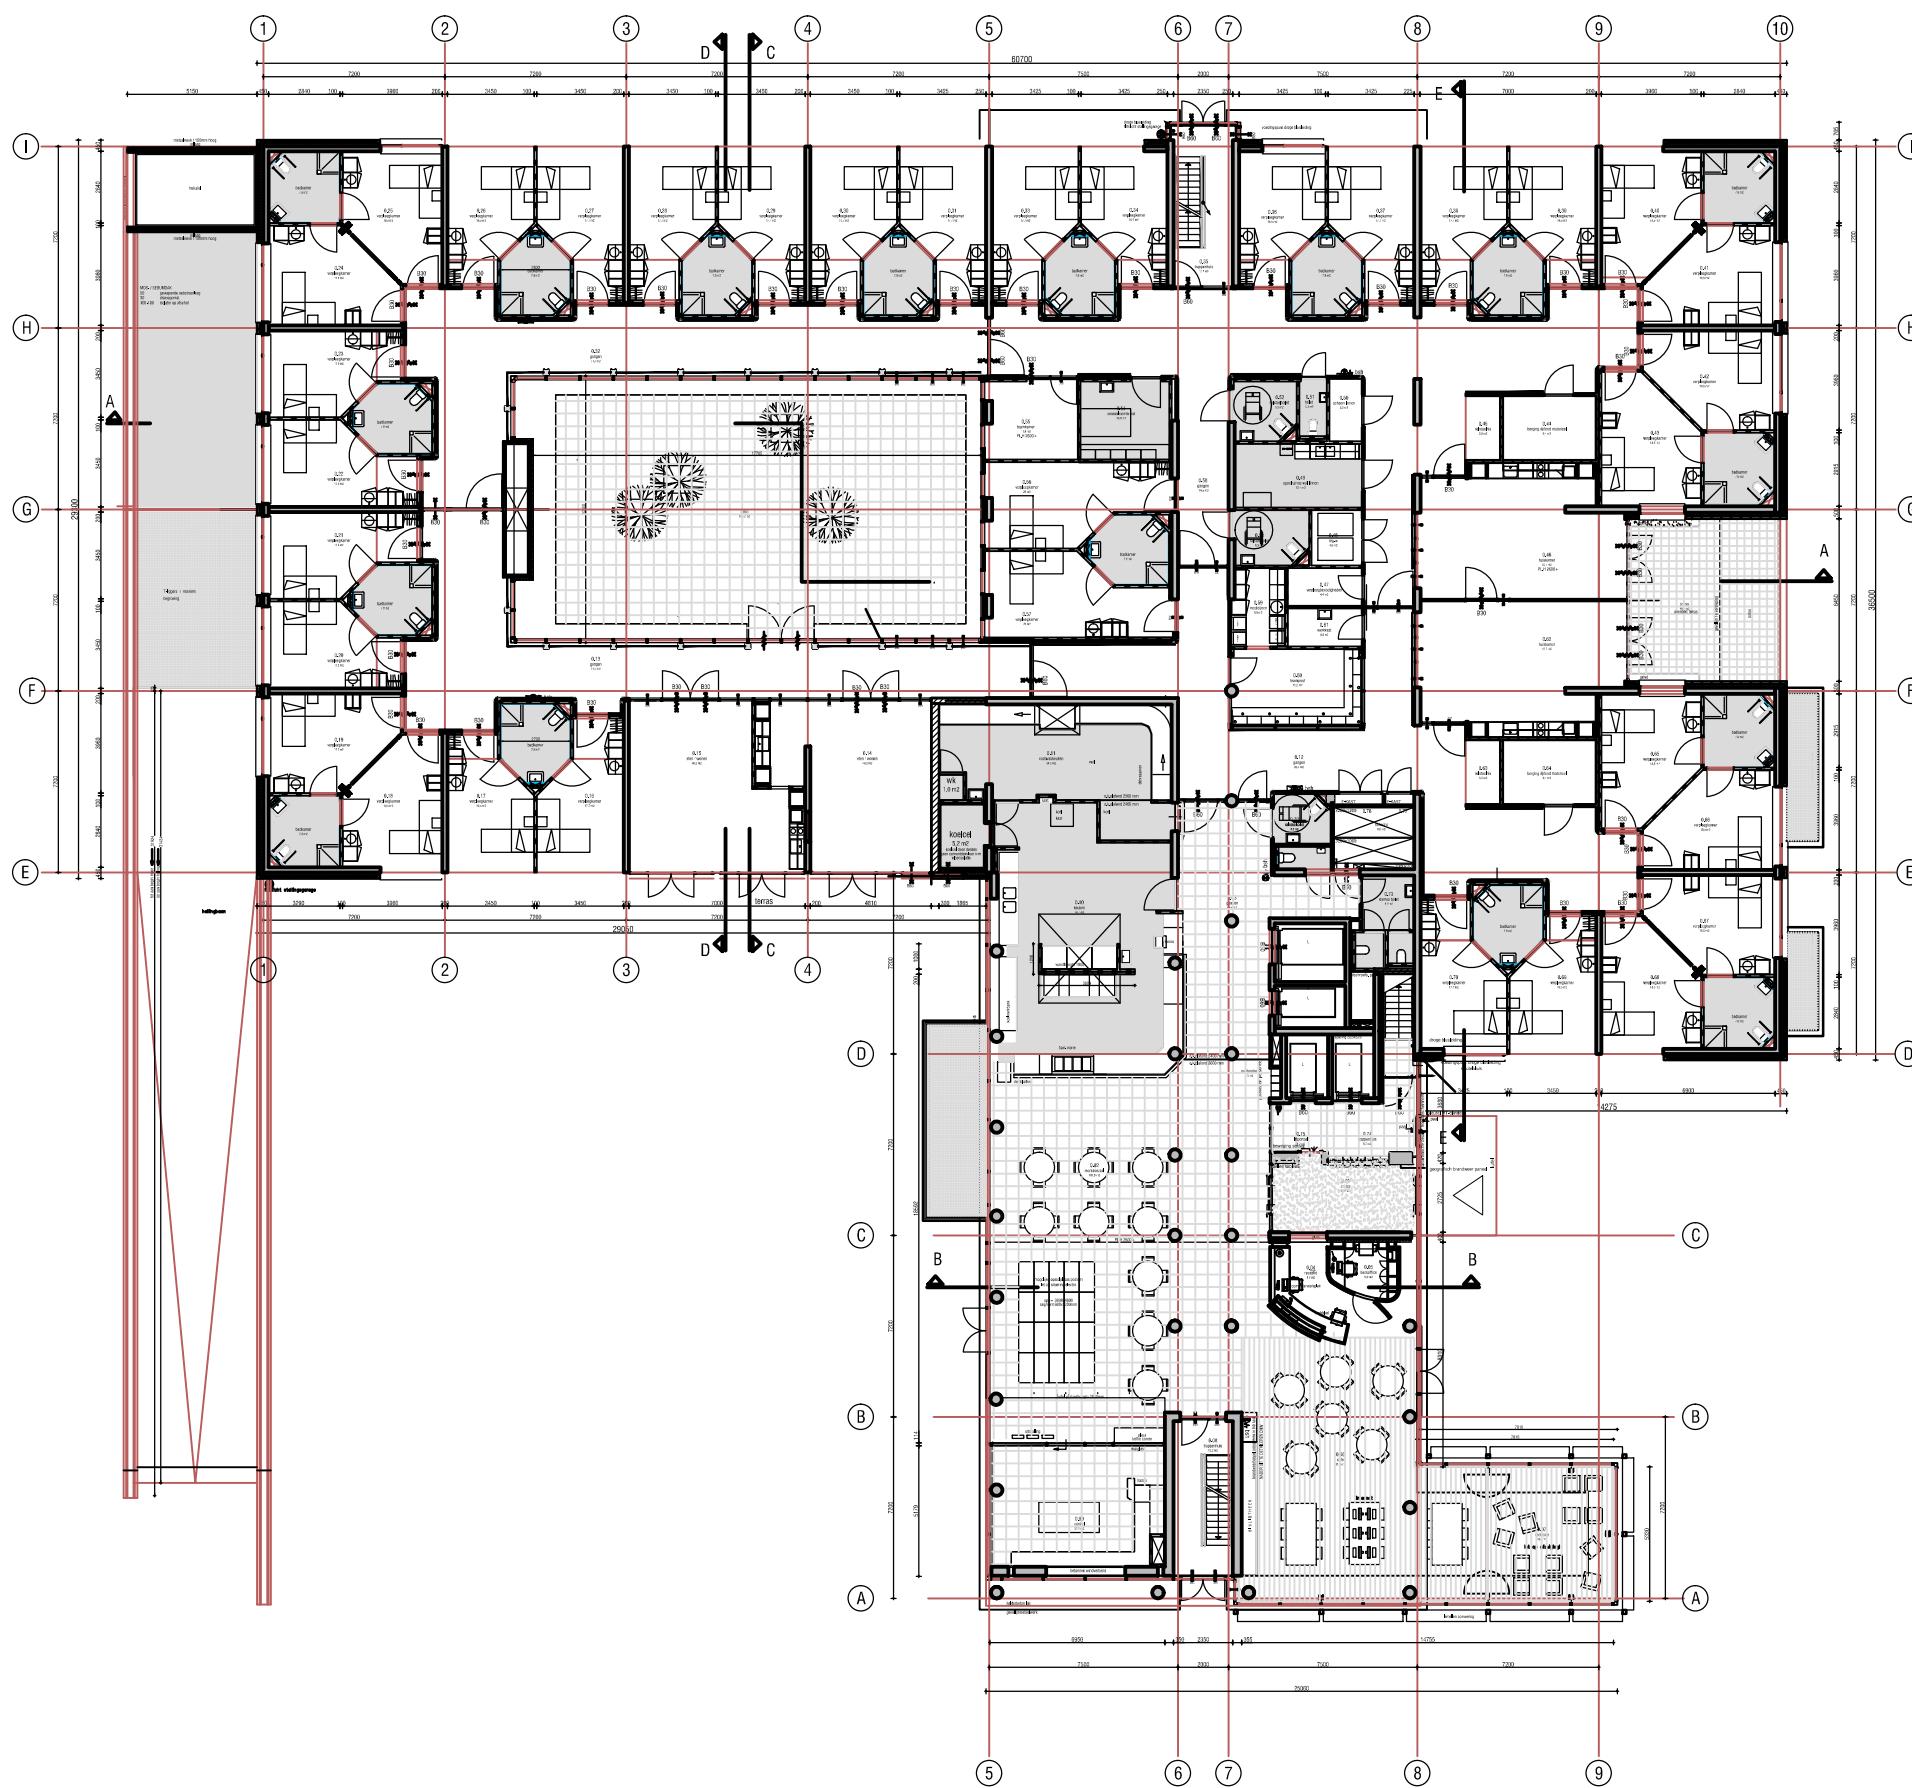

Plattegrond Eerste Verdieping

Tek.no.:

2c

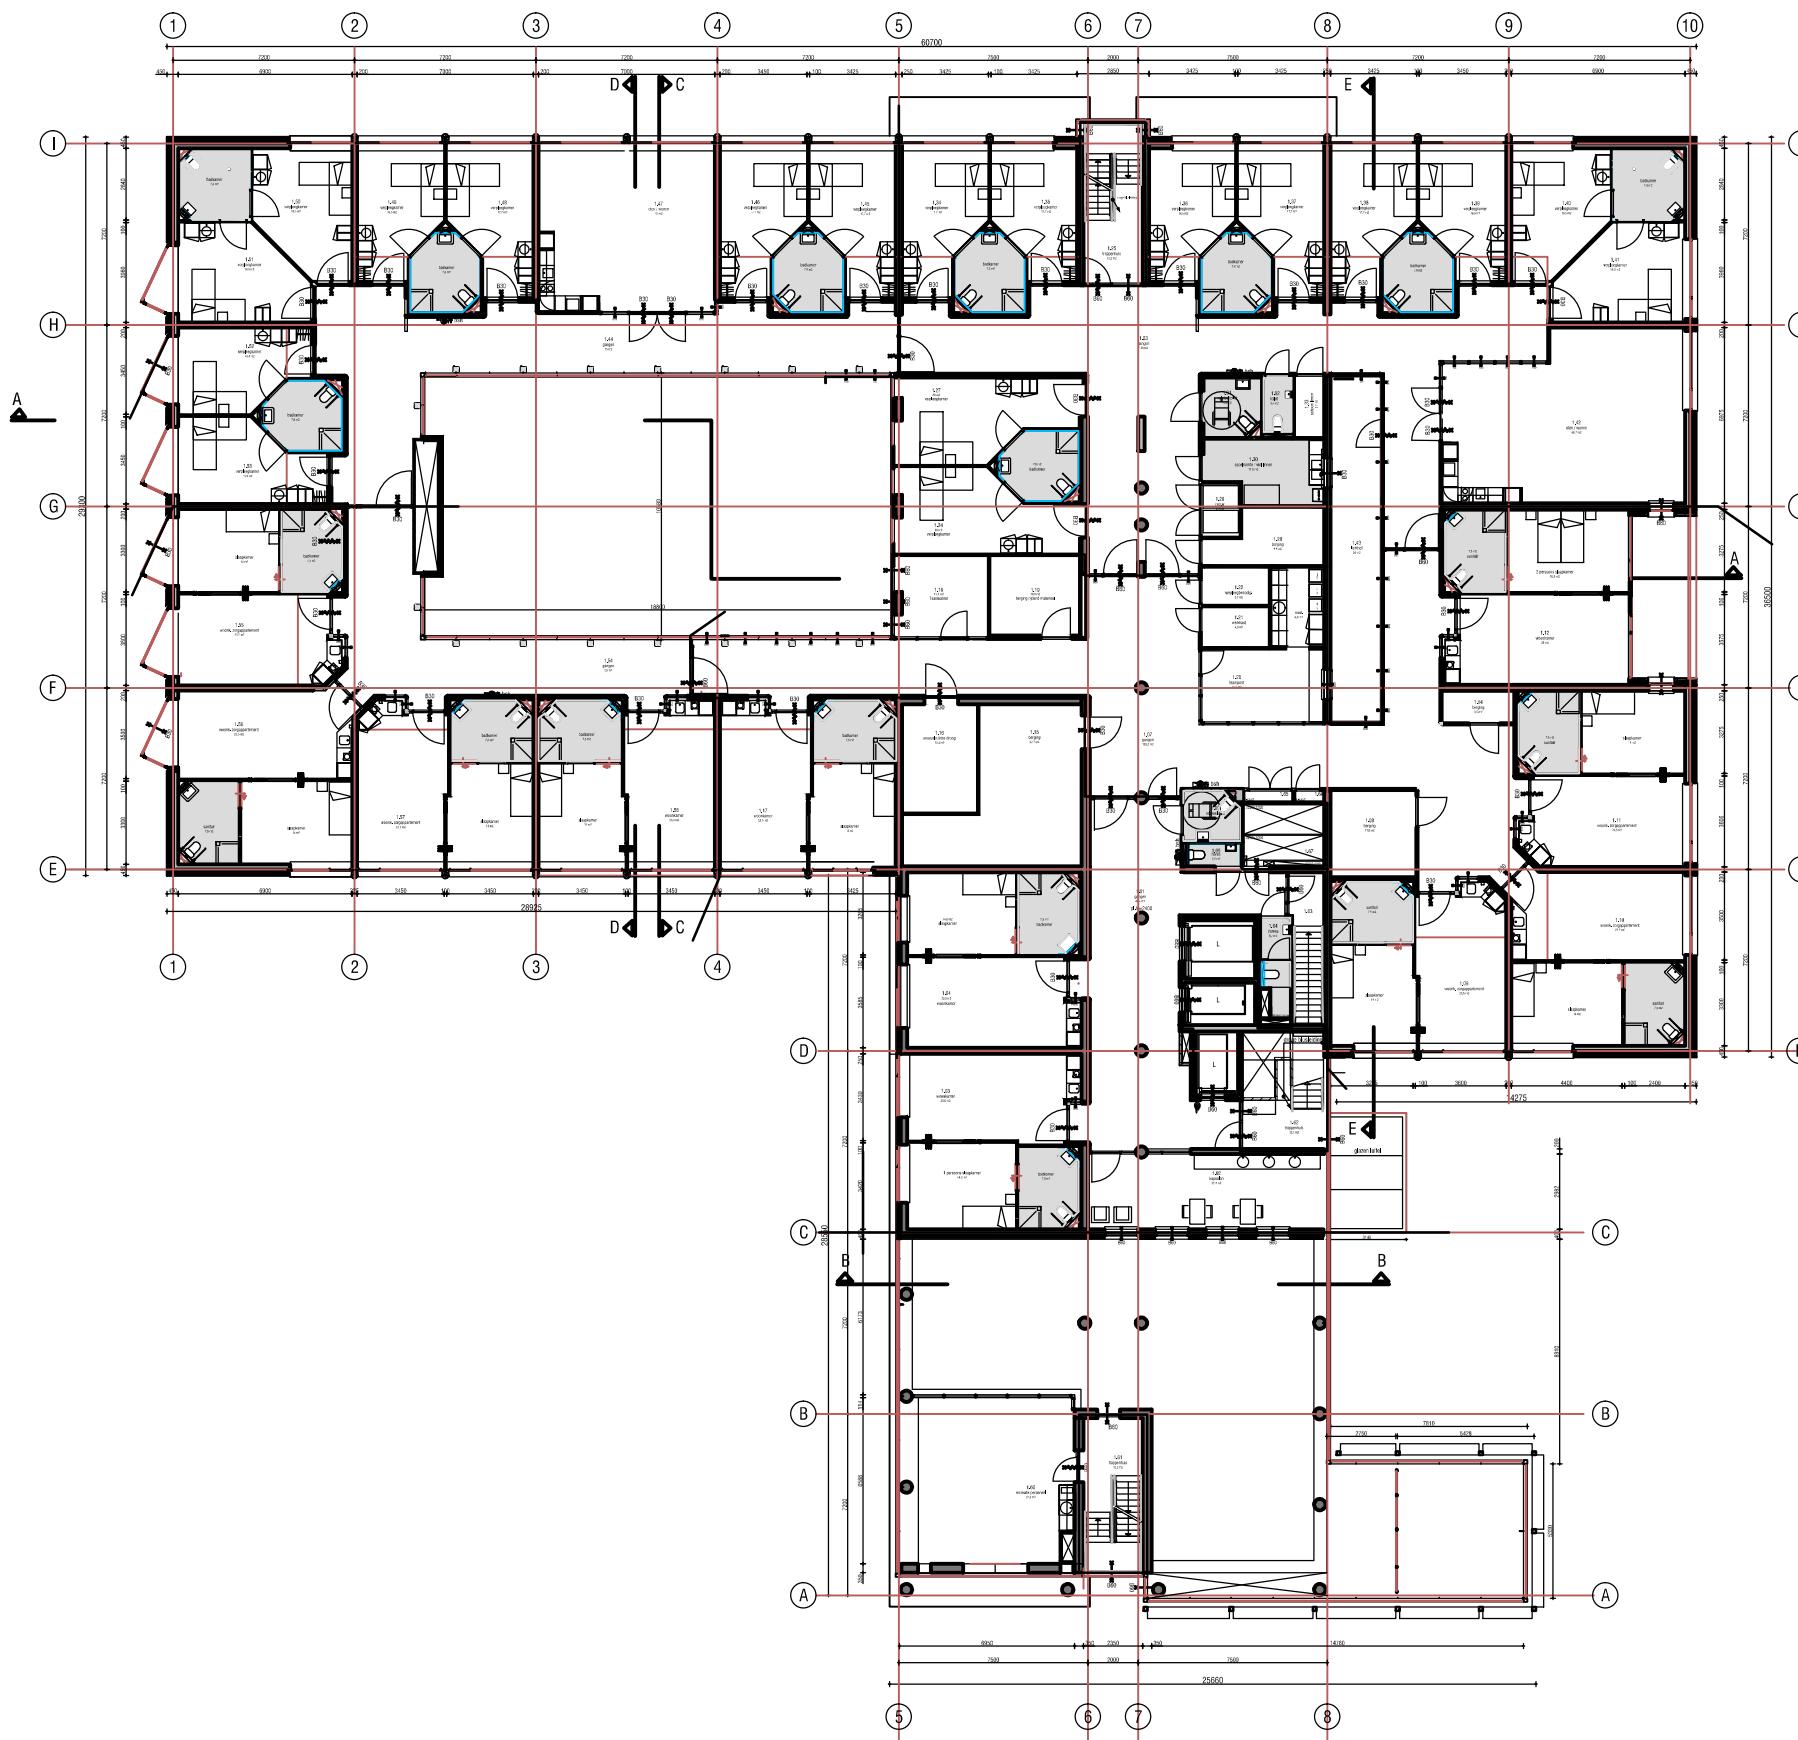

BrabantWonen  
Postbus 151  
5340AD OSS  
info@brabantwonen.nl


## Wooncomplex Nieuwehagen

Woonzorgcentrum met 31 appartementen

### Plattegrond Tweede Verdieping

Tek.no.: 2d

Schaal: 1 a 300  
Formaat: A3  
Get.: mka  
Gew.: dec 2006

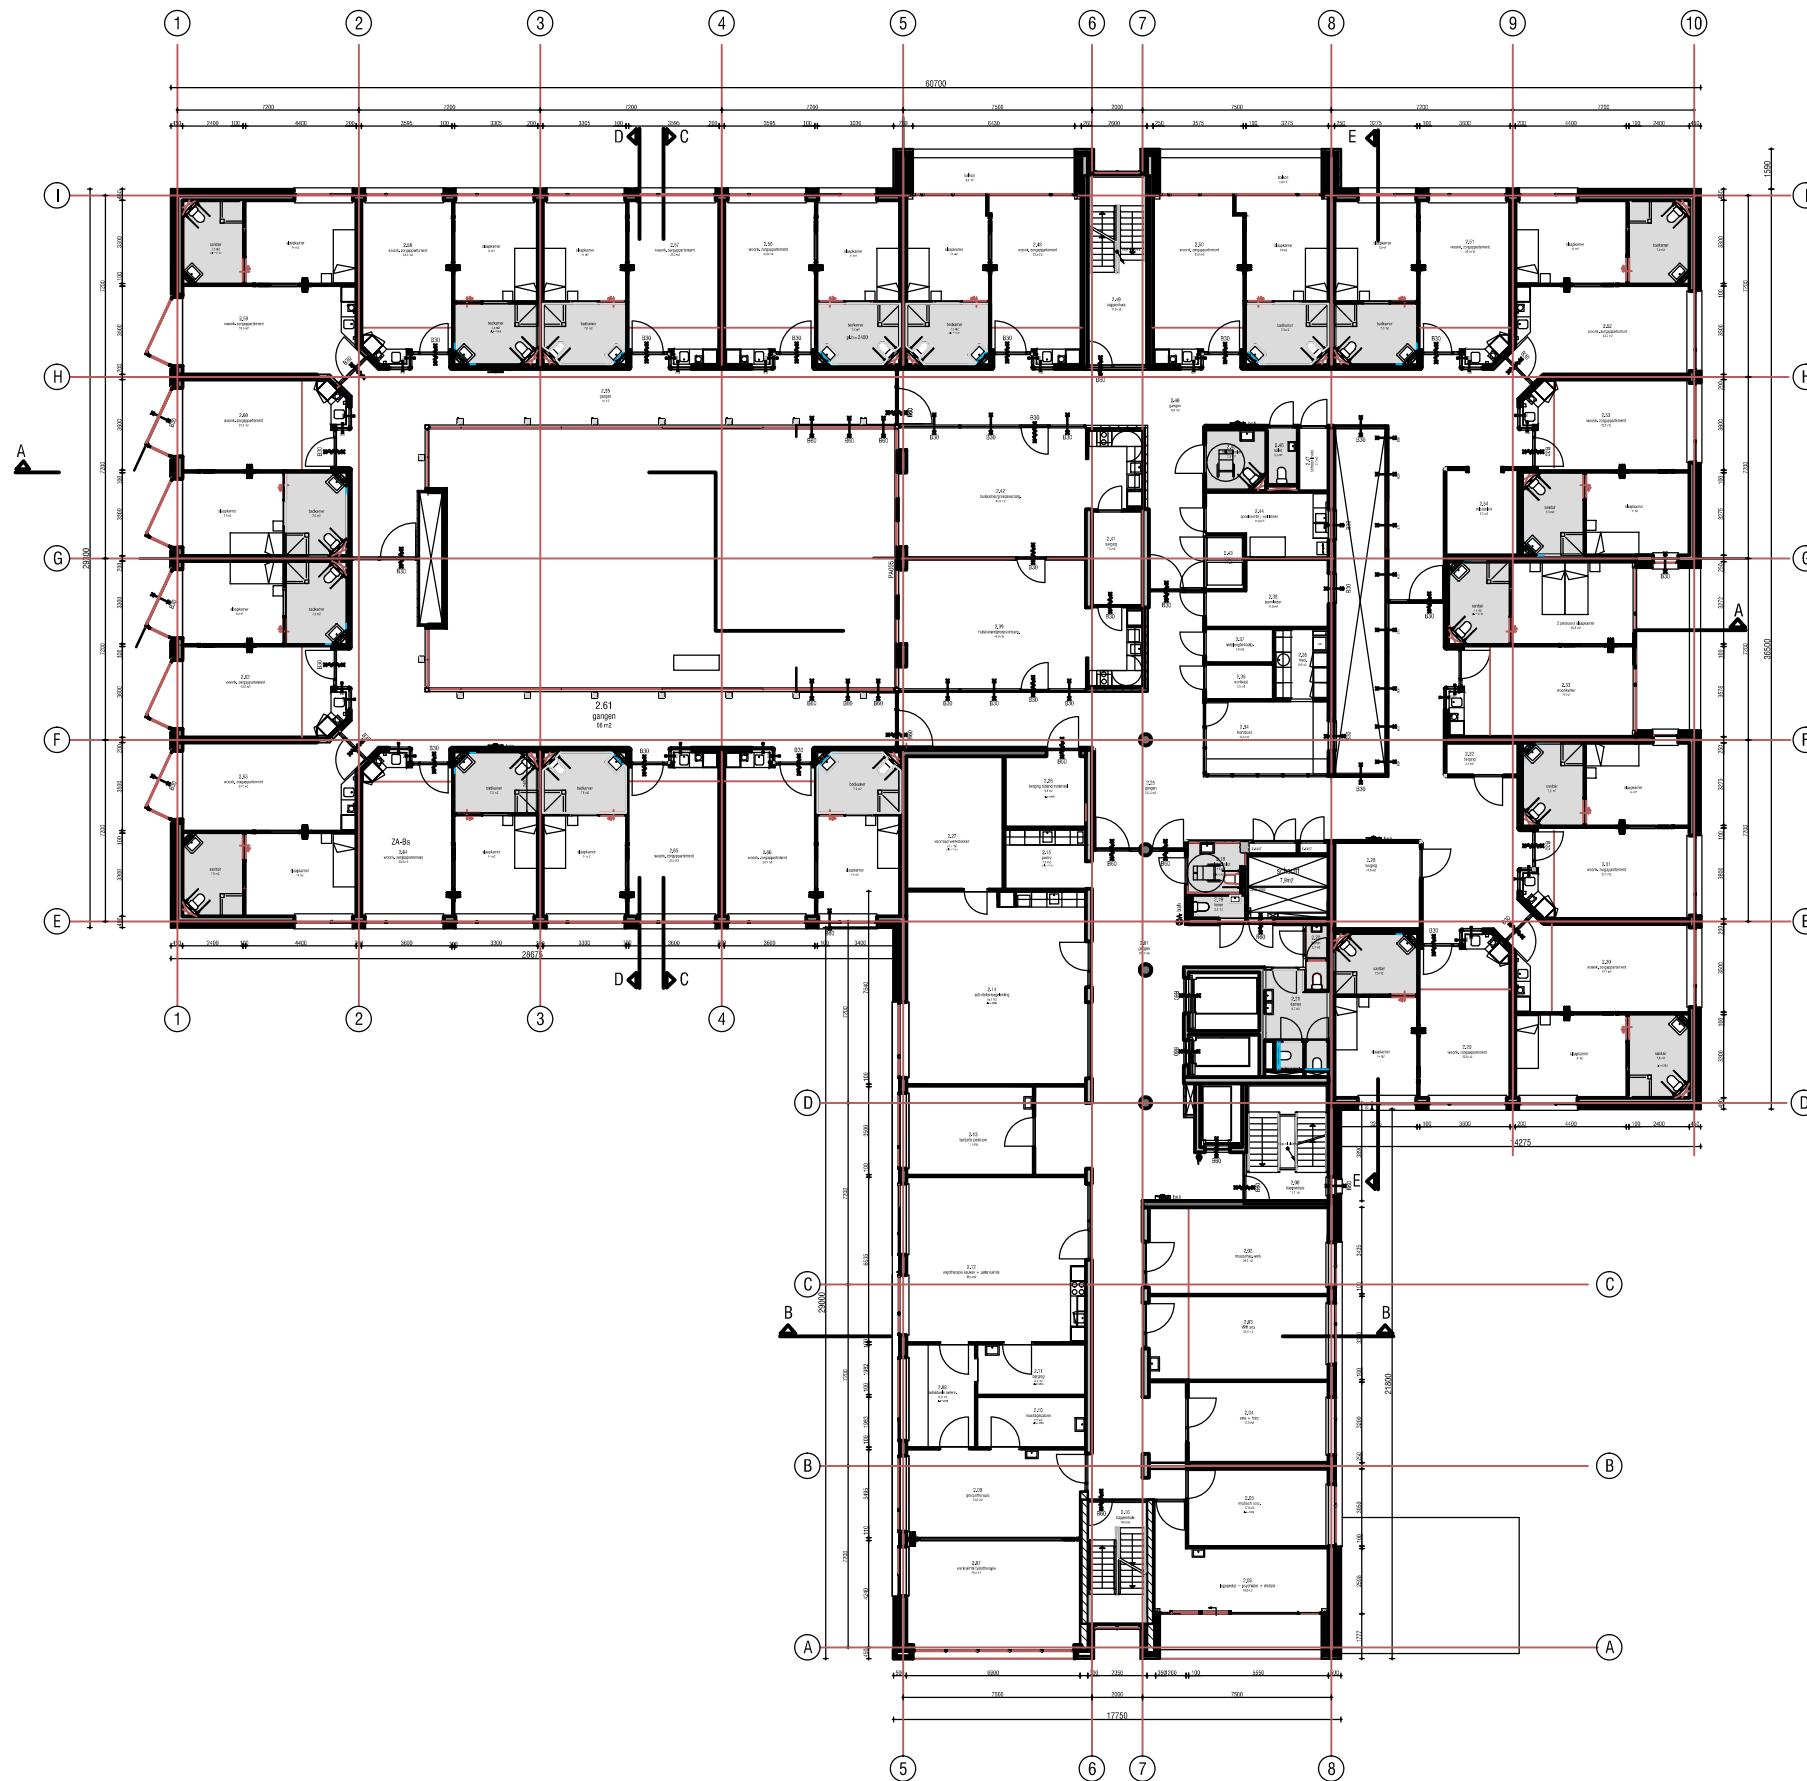


BrabantWonen  
Postbus 151  
5340AD OSS  
info@brabantwonen.nl

## Wooncomplex Nieuwehagen

Woonzorgcentrum met 31 appartementen

### Plattegrond Derde Verdieping

Tek.no.: 2e

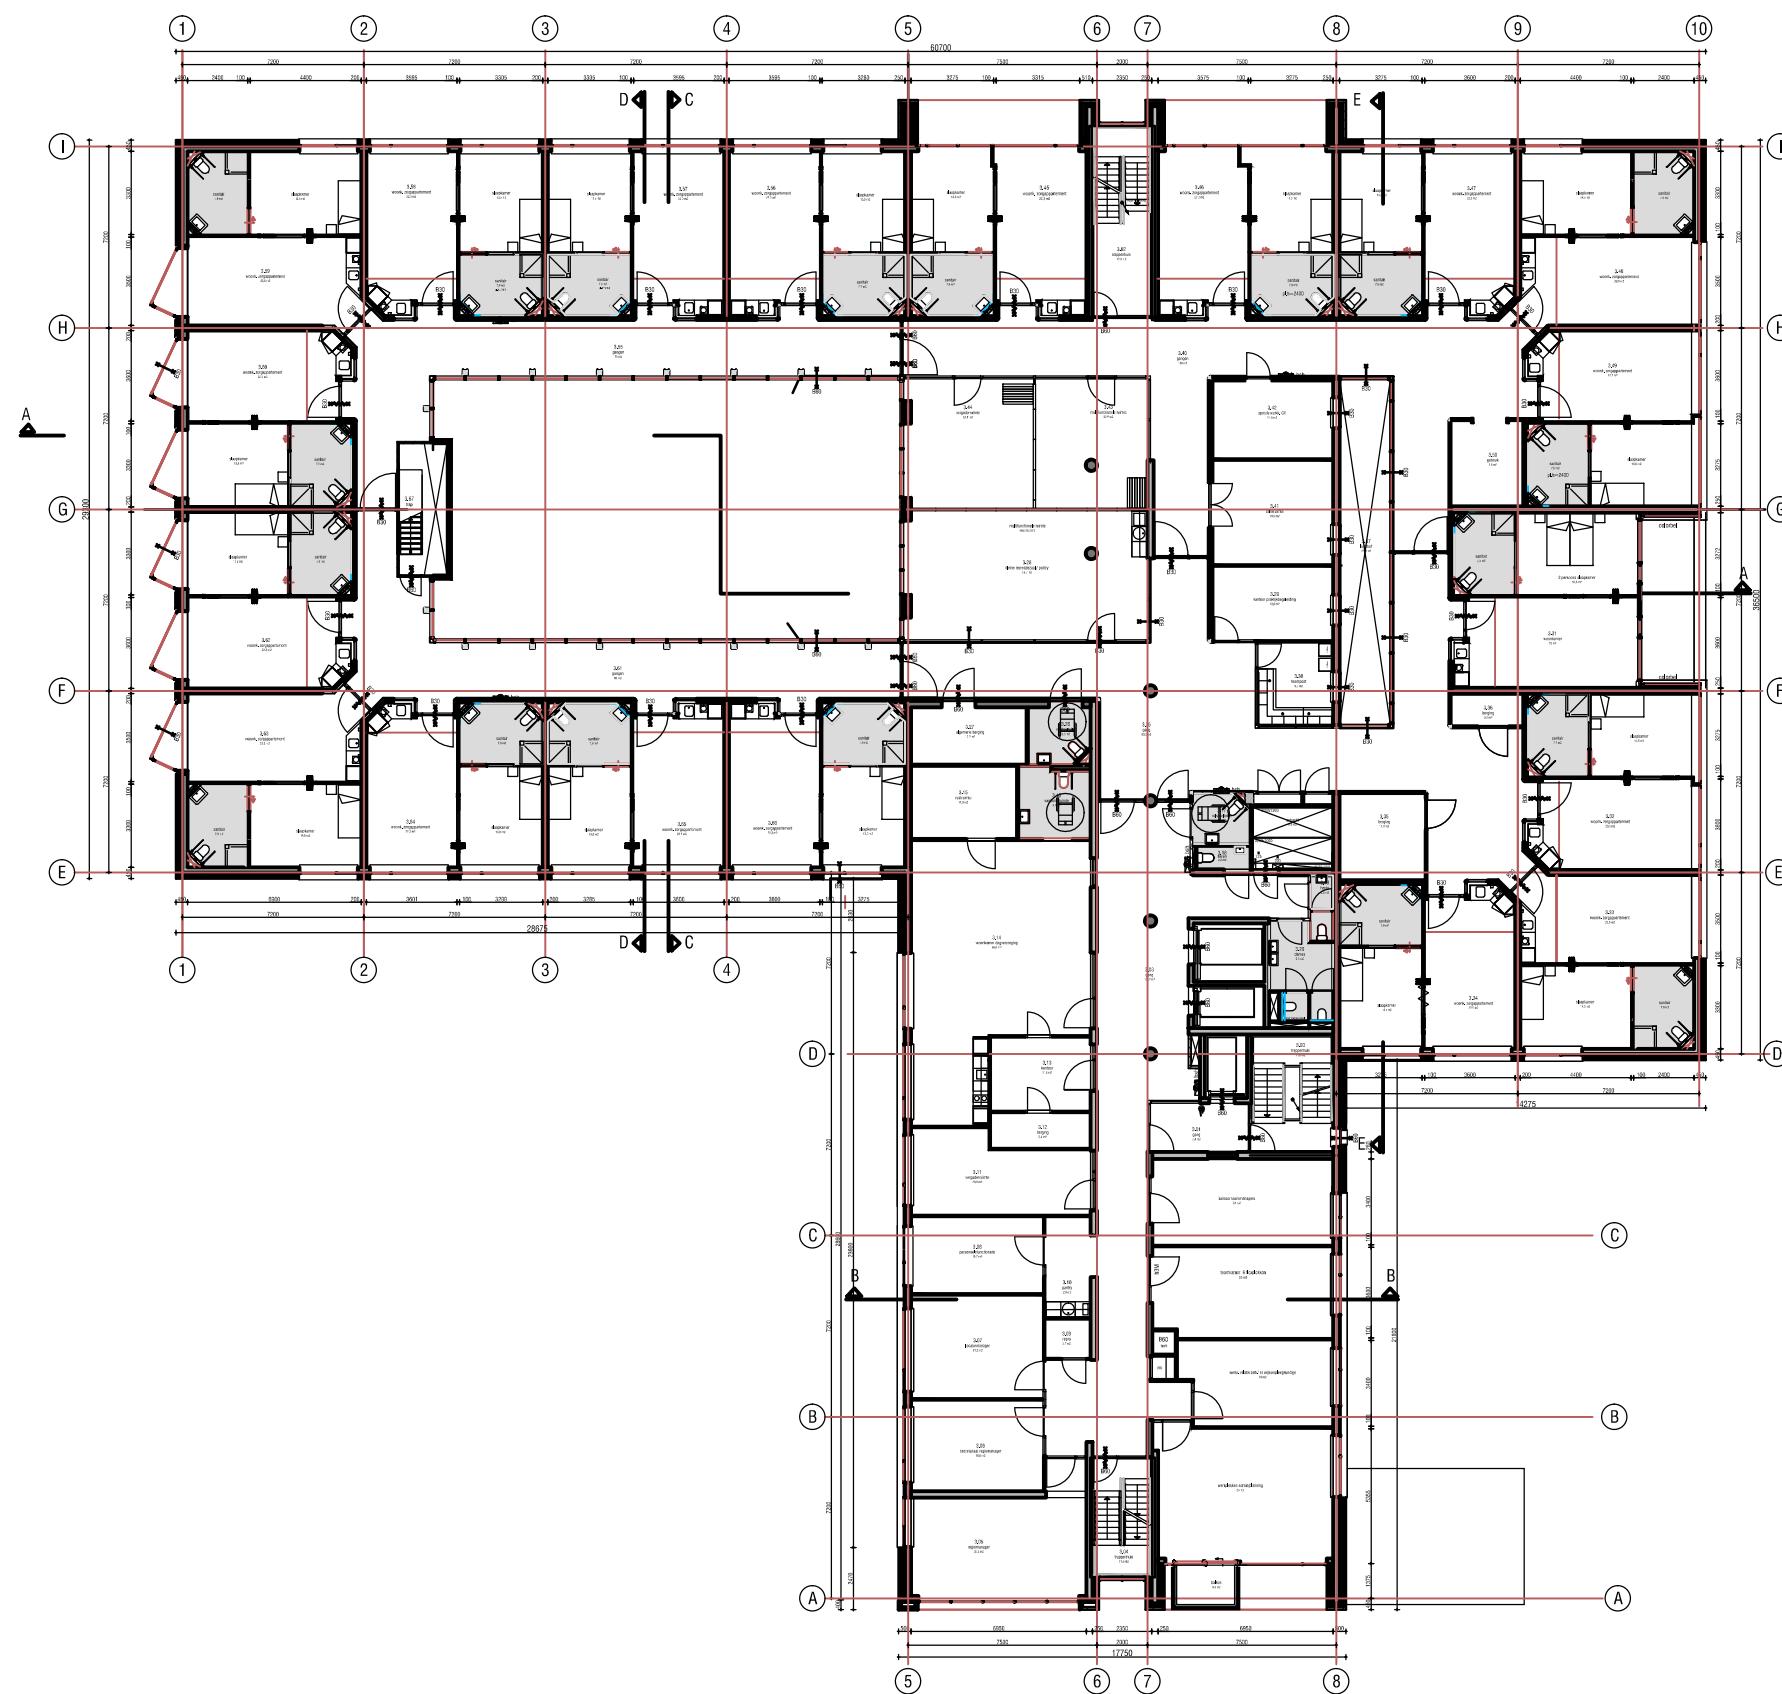


Plattegrond 4e verdieping met huisnummers

Tek.no.:

2



Schaal:	1 a 200
Formaat:	A3
Get.:	mka
Gew.:	dec 2006

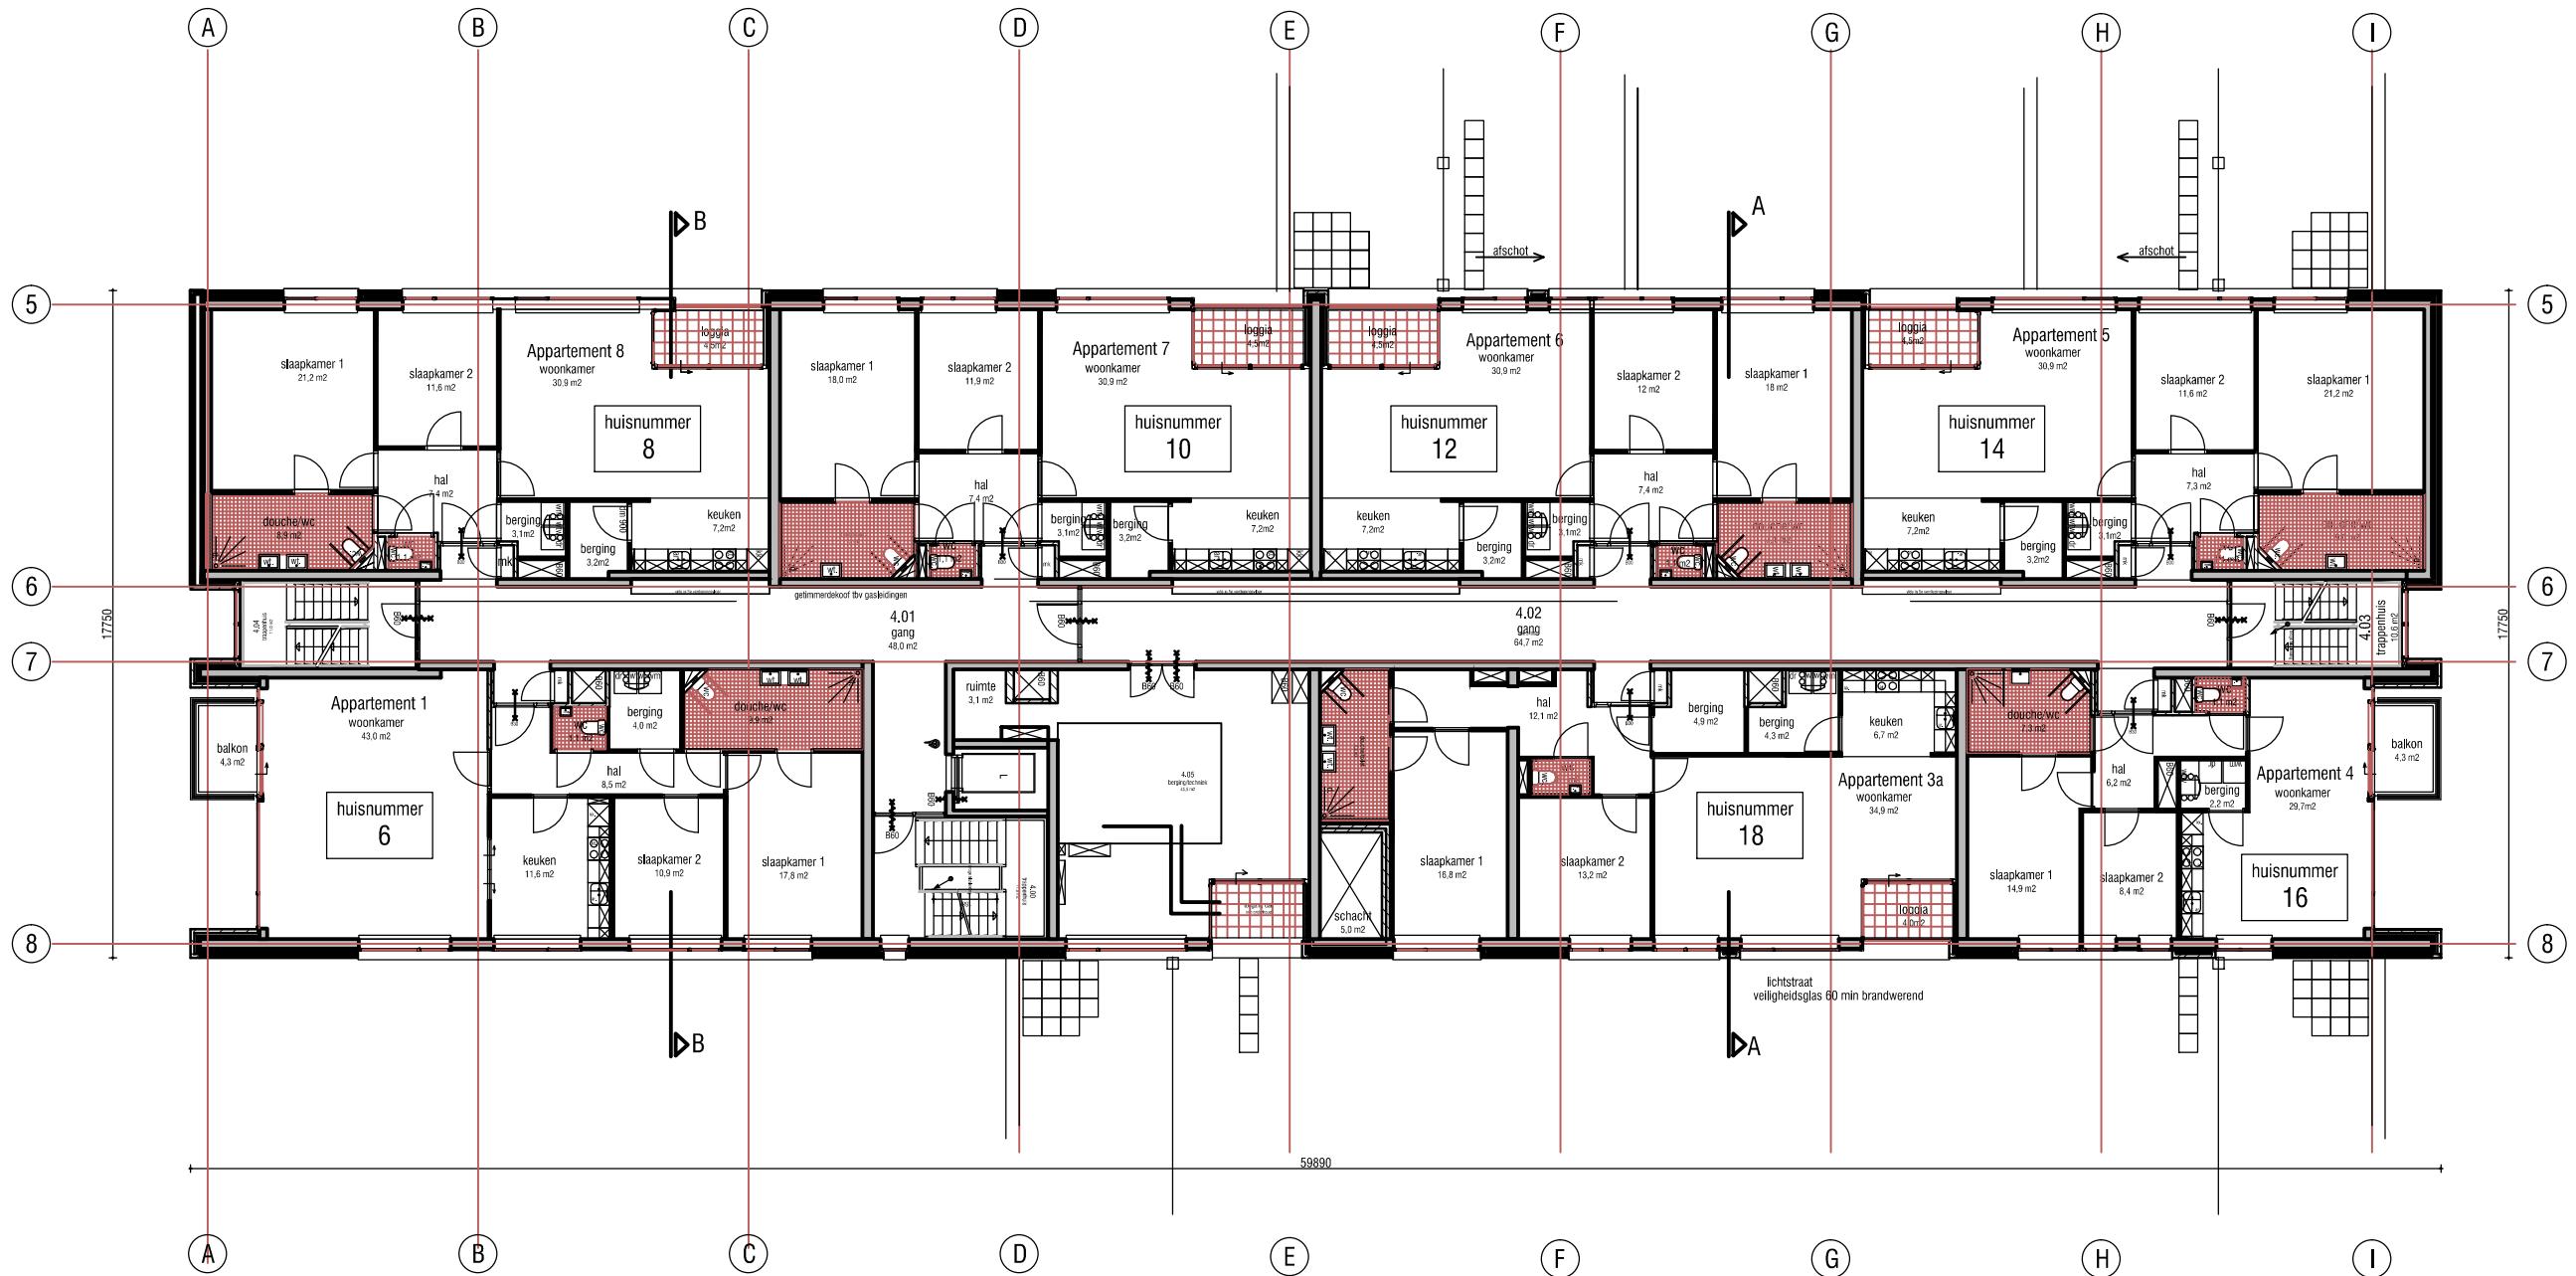


Plattegrond 5e verdieping met huisnummers

Tek.no.:

3

Schaal:	1 a 200
Formaat:	A3
Get.:	mka
Gew.:	dec 2006

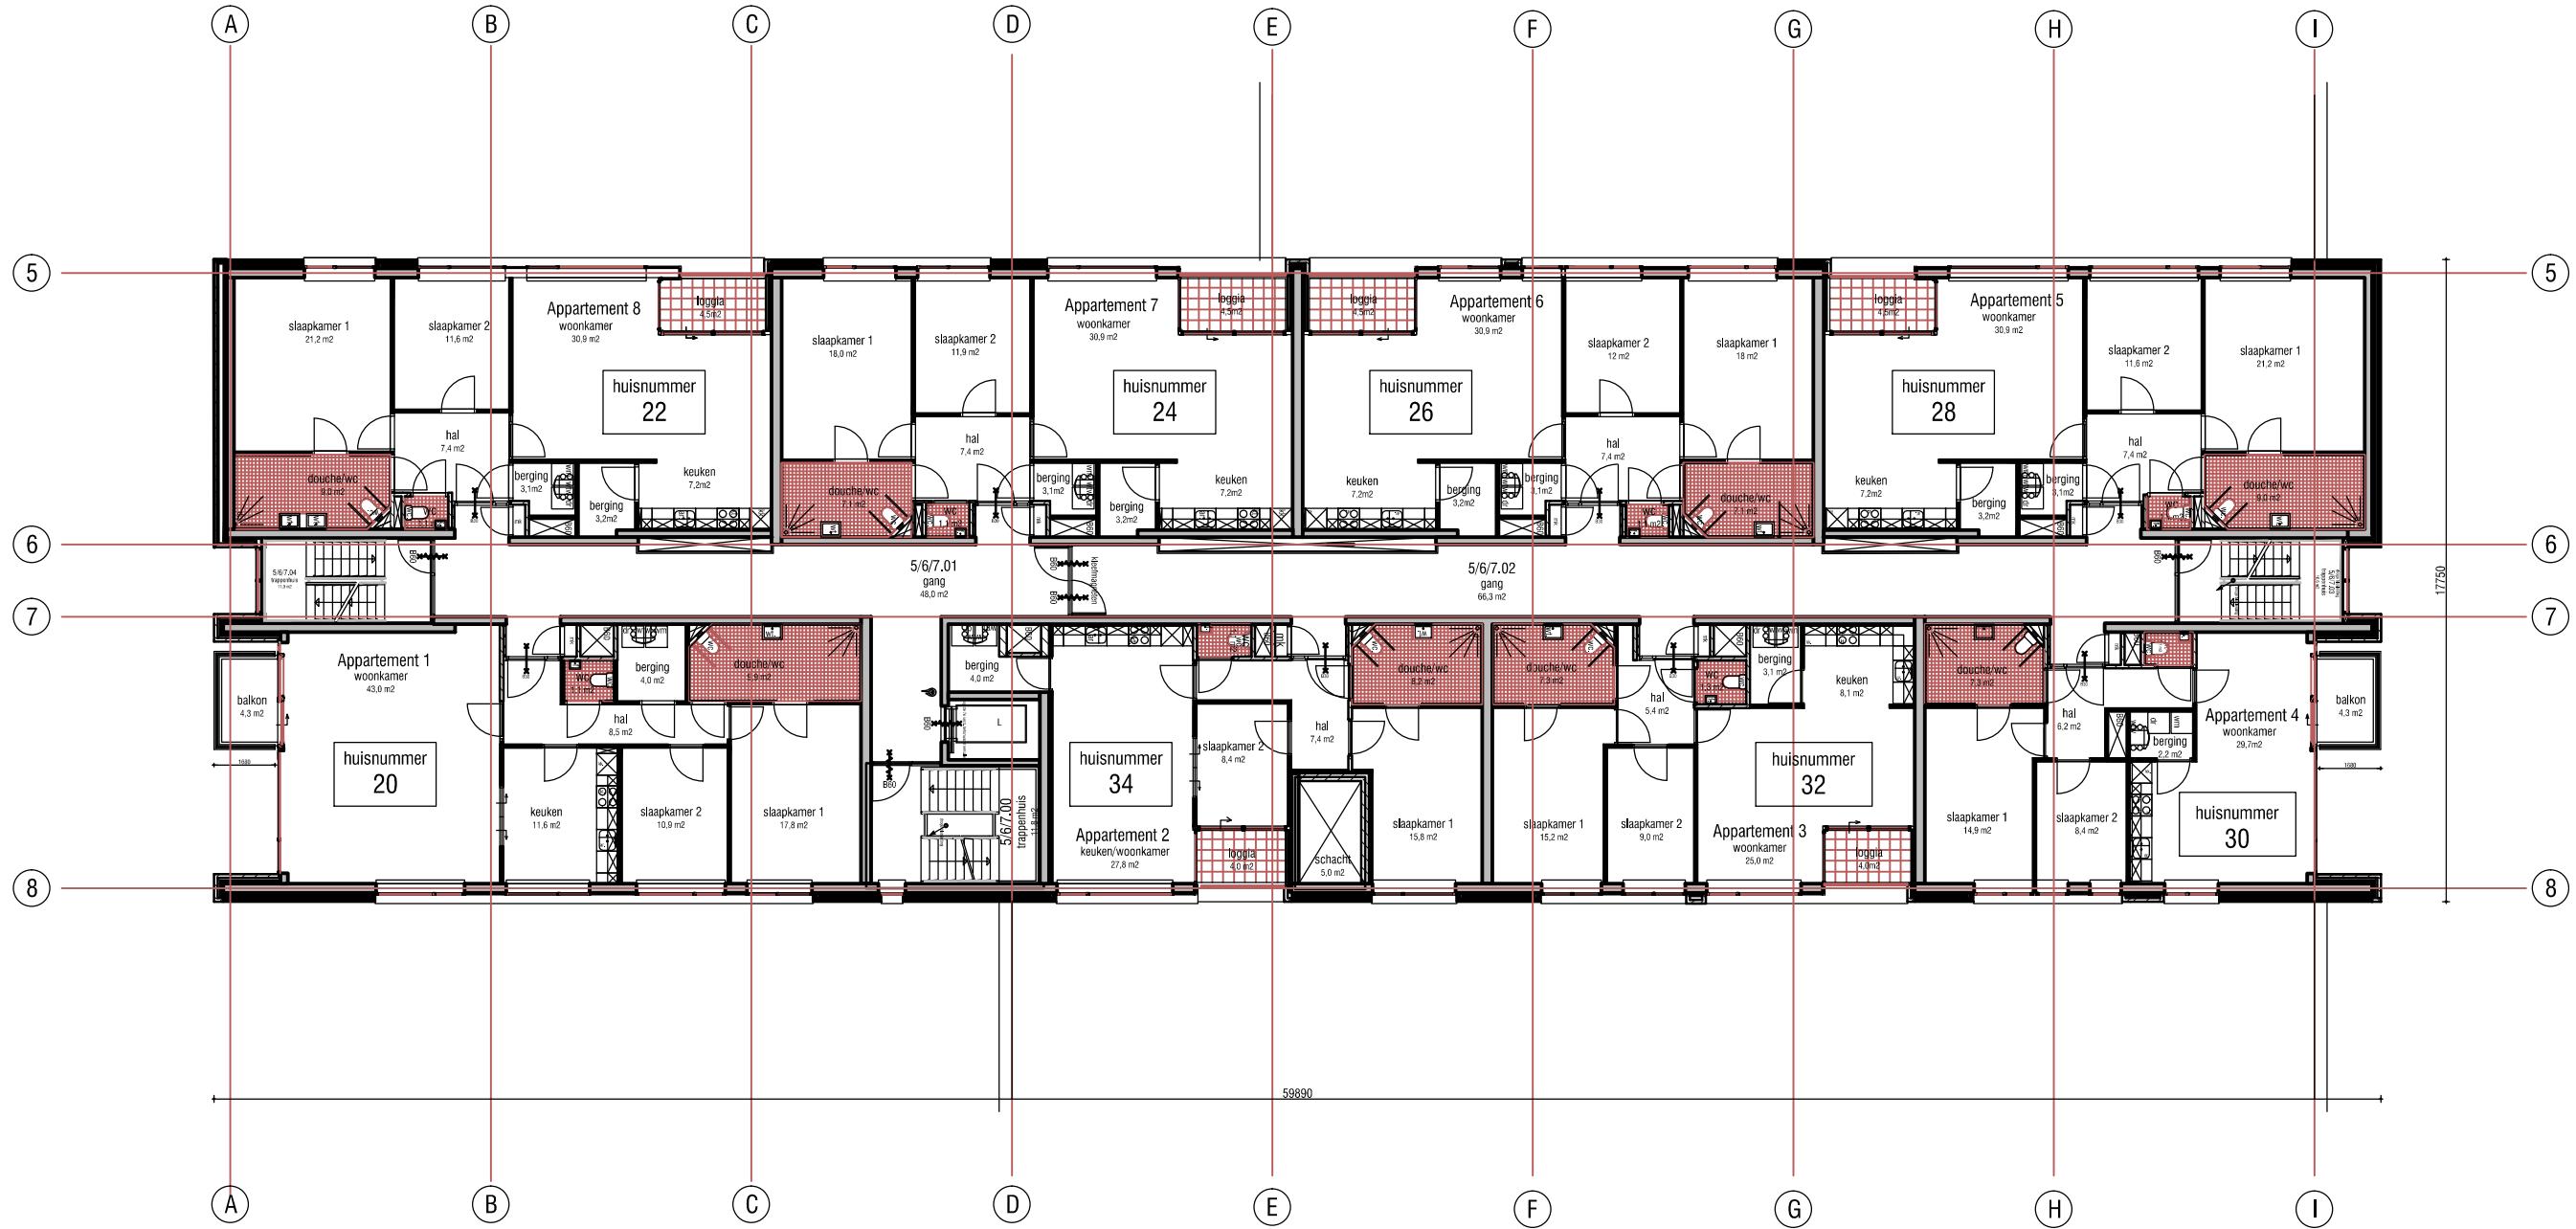


Plattegrond 6e verdieping met huisnummers

Tek.no.:

4



Schaal: 1 a 200  
Formaat: A3  
Get.: mka  
Gew.: dec 2006

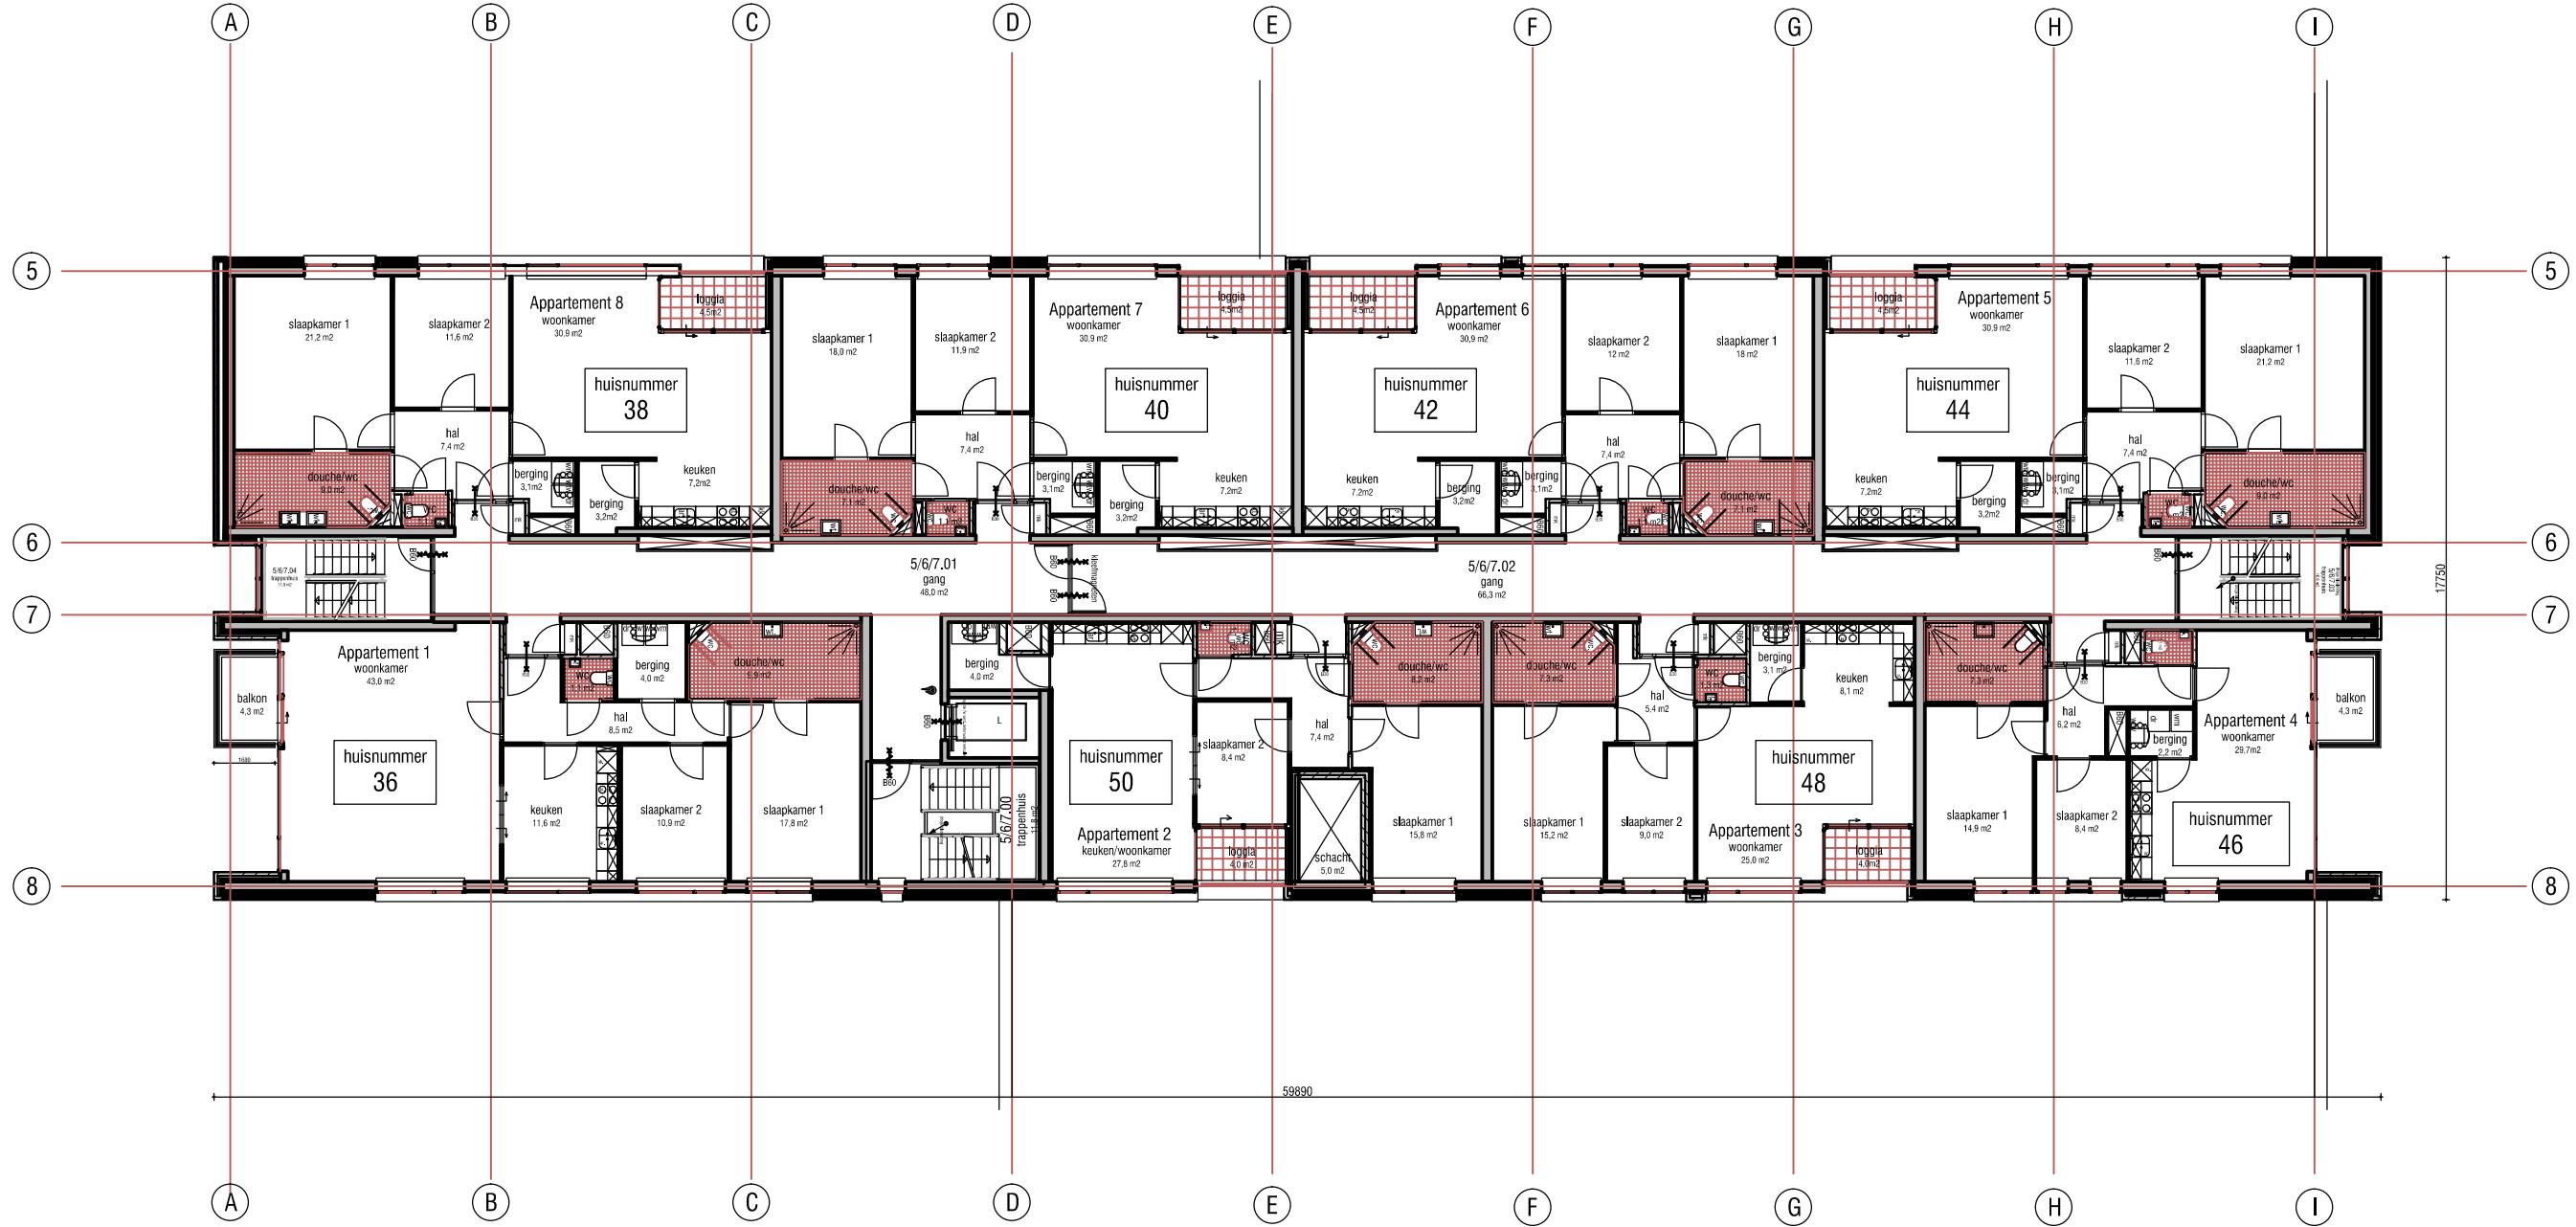


Plattegrond 7e verdieping met huisnummers

Tek.no.:

5


Schaal:	1 a 200	Brabant Wonen
Formaat:	A3	
Get.:	mka	
Gew.:	dec 2006	

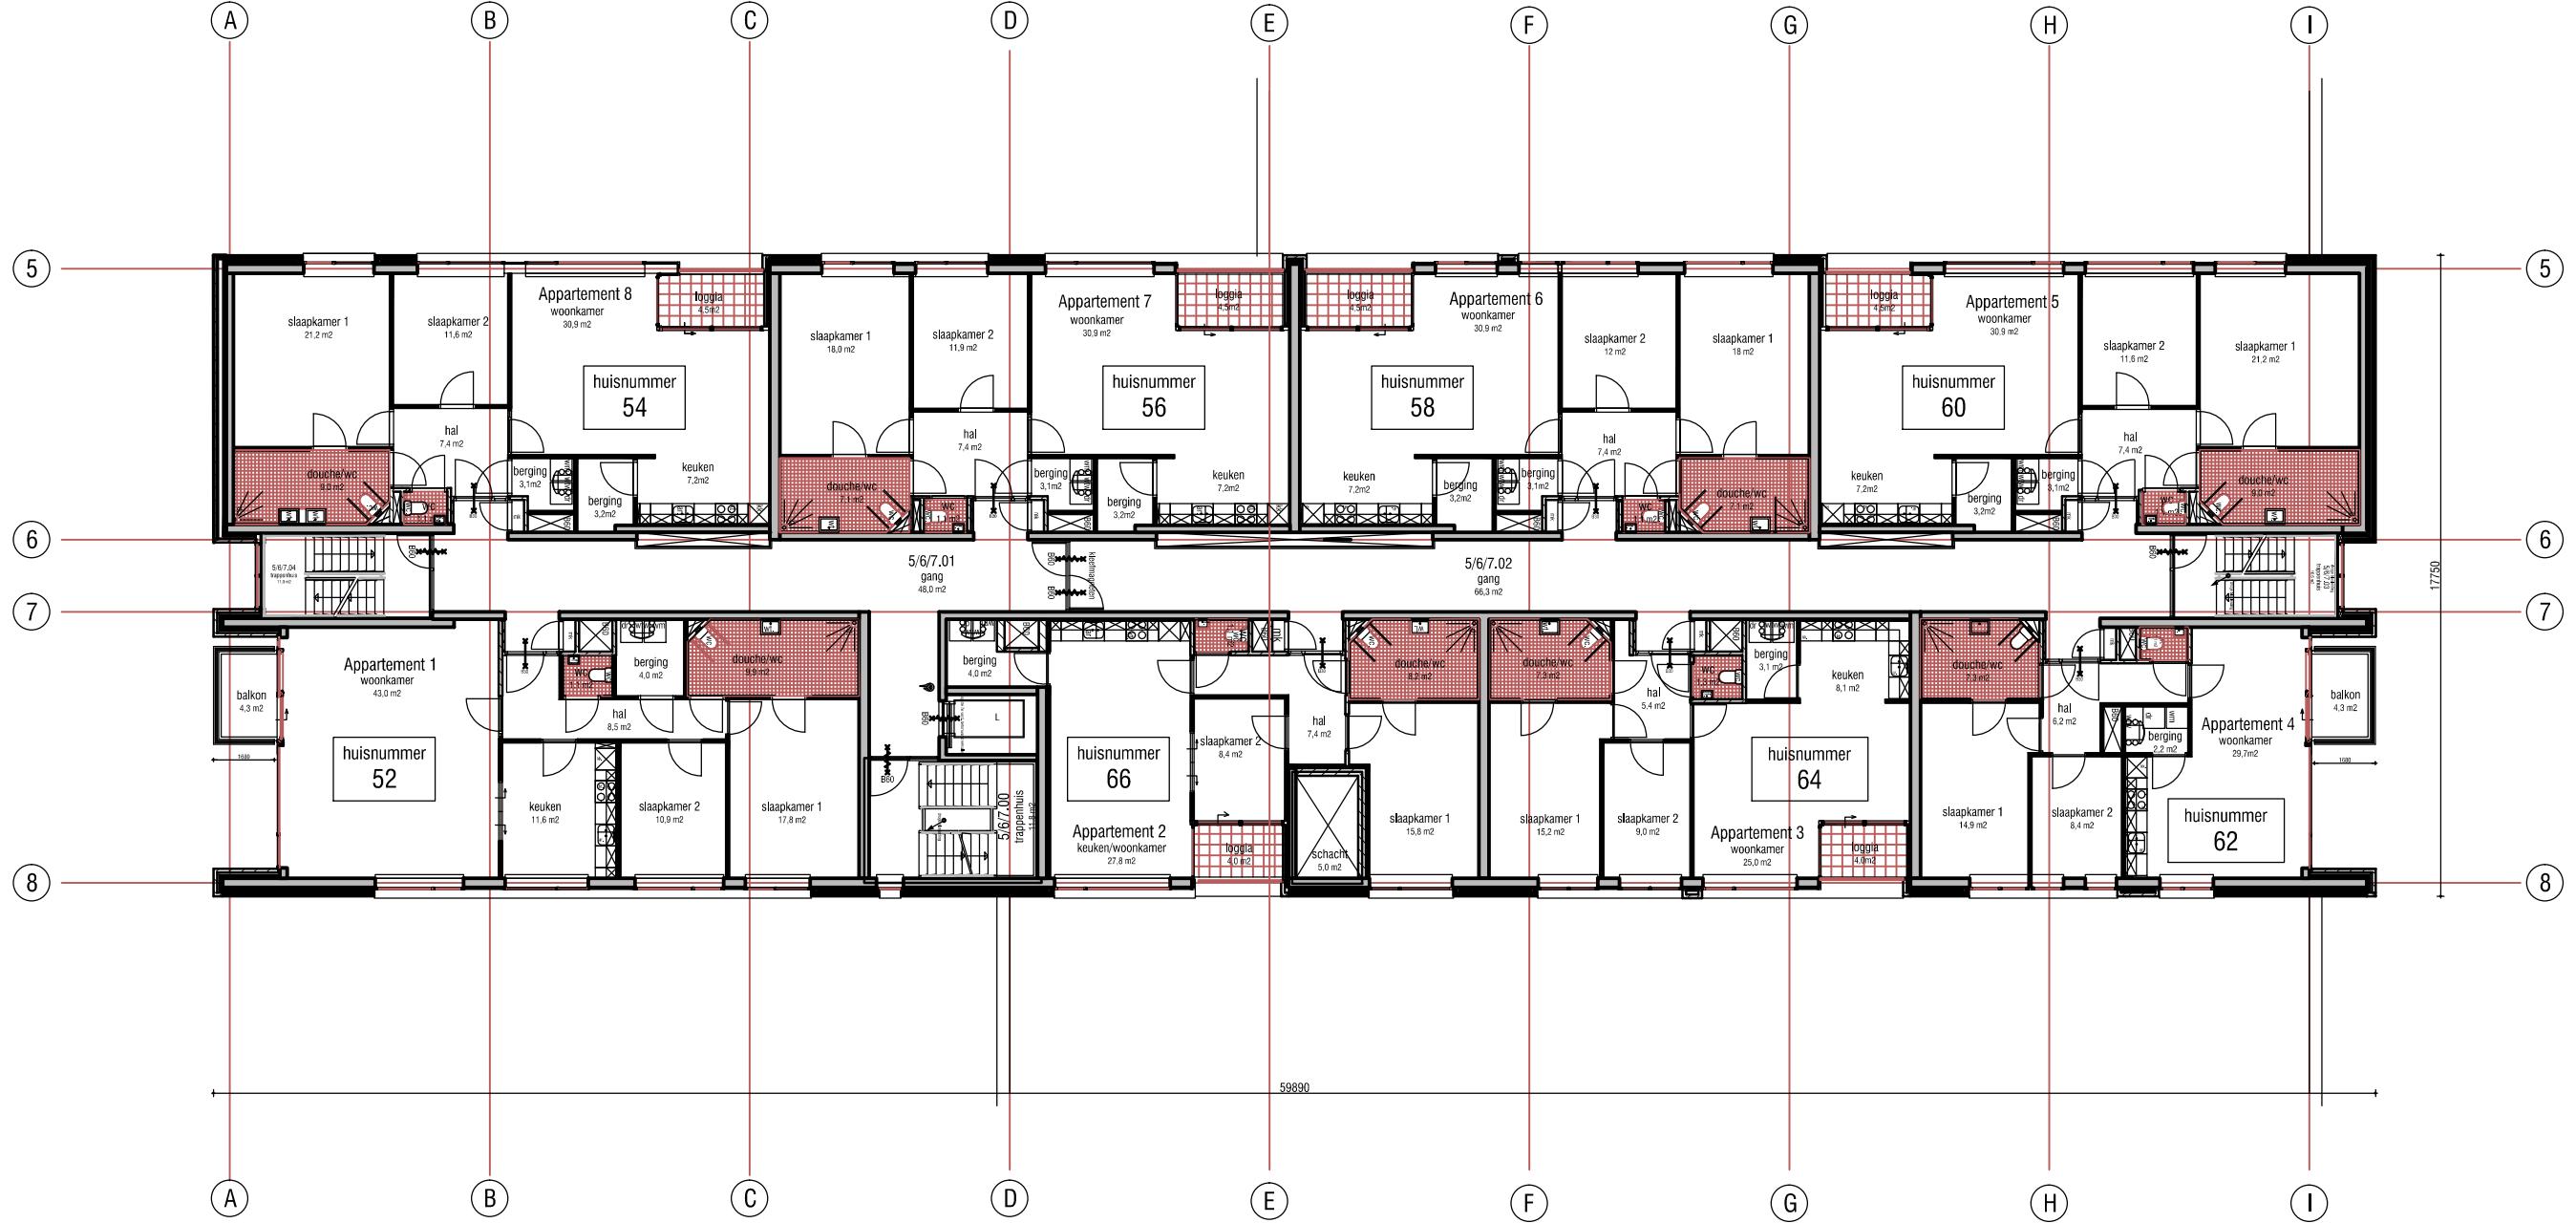

Gevelaanzingten

Tek.no.:

6

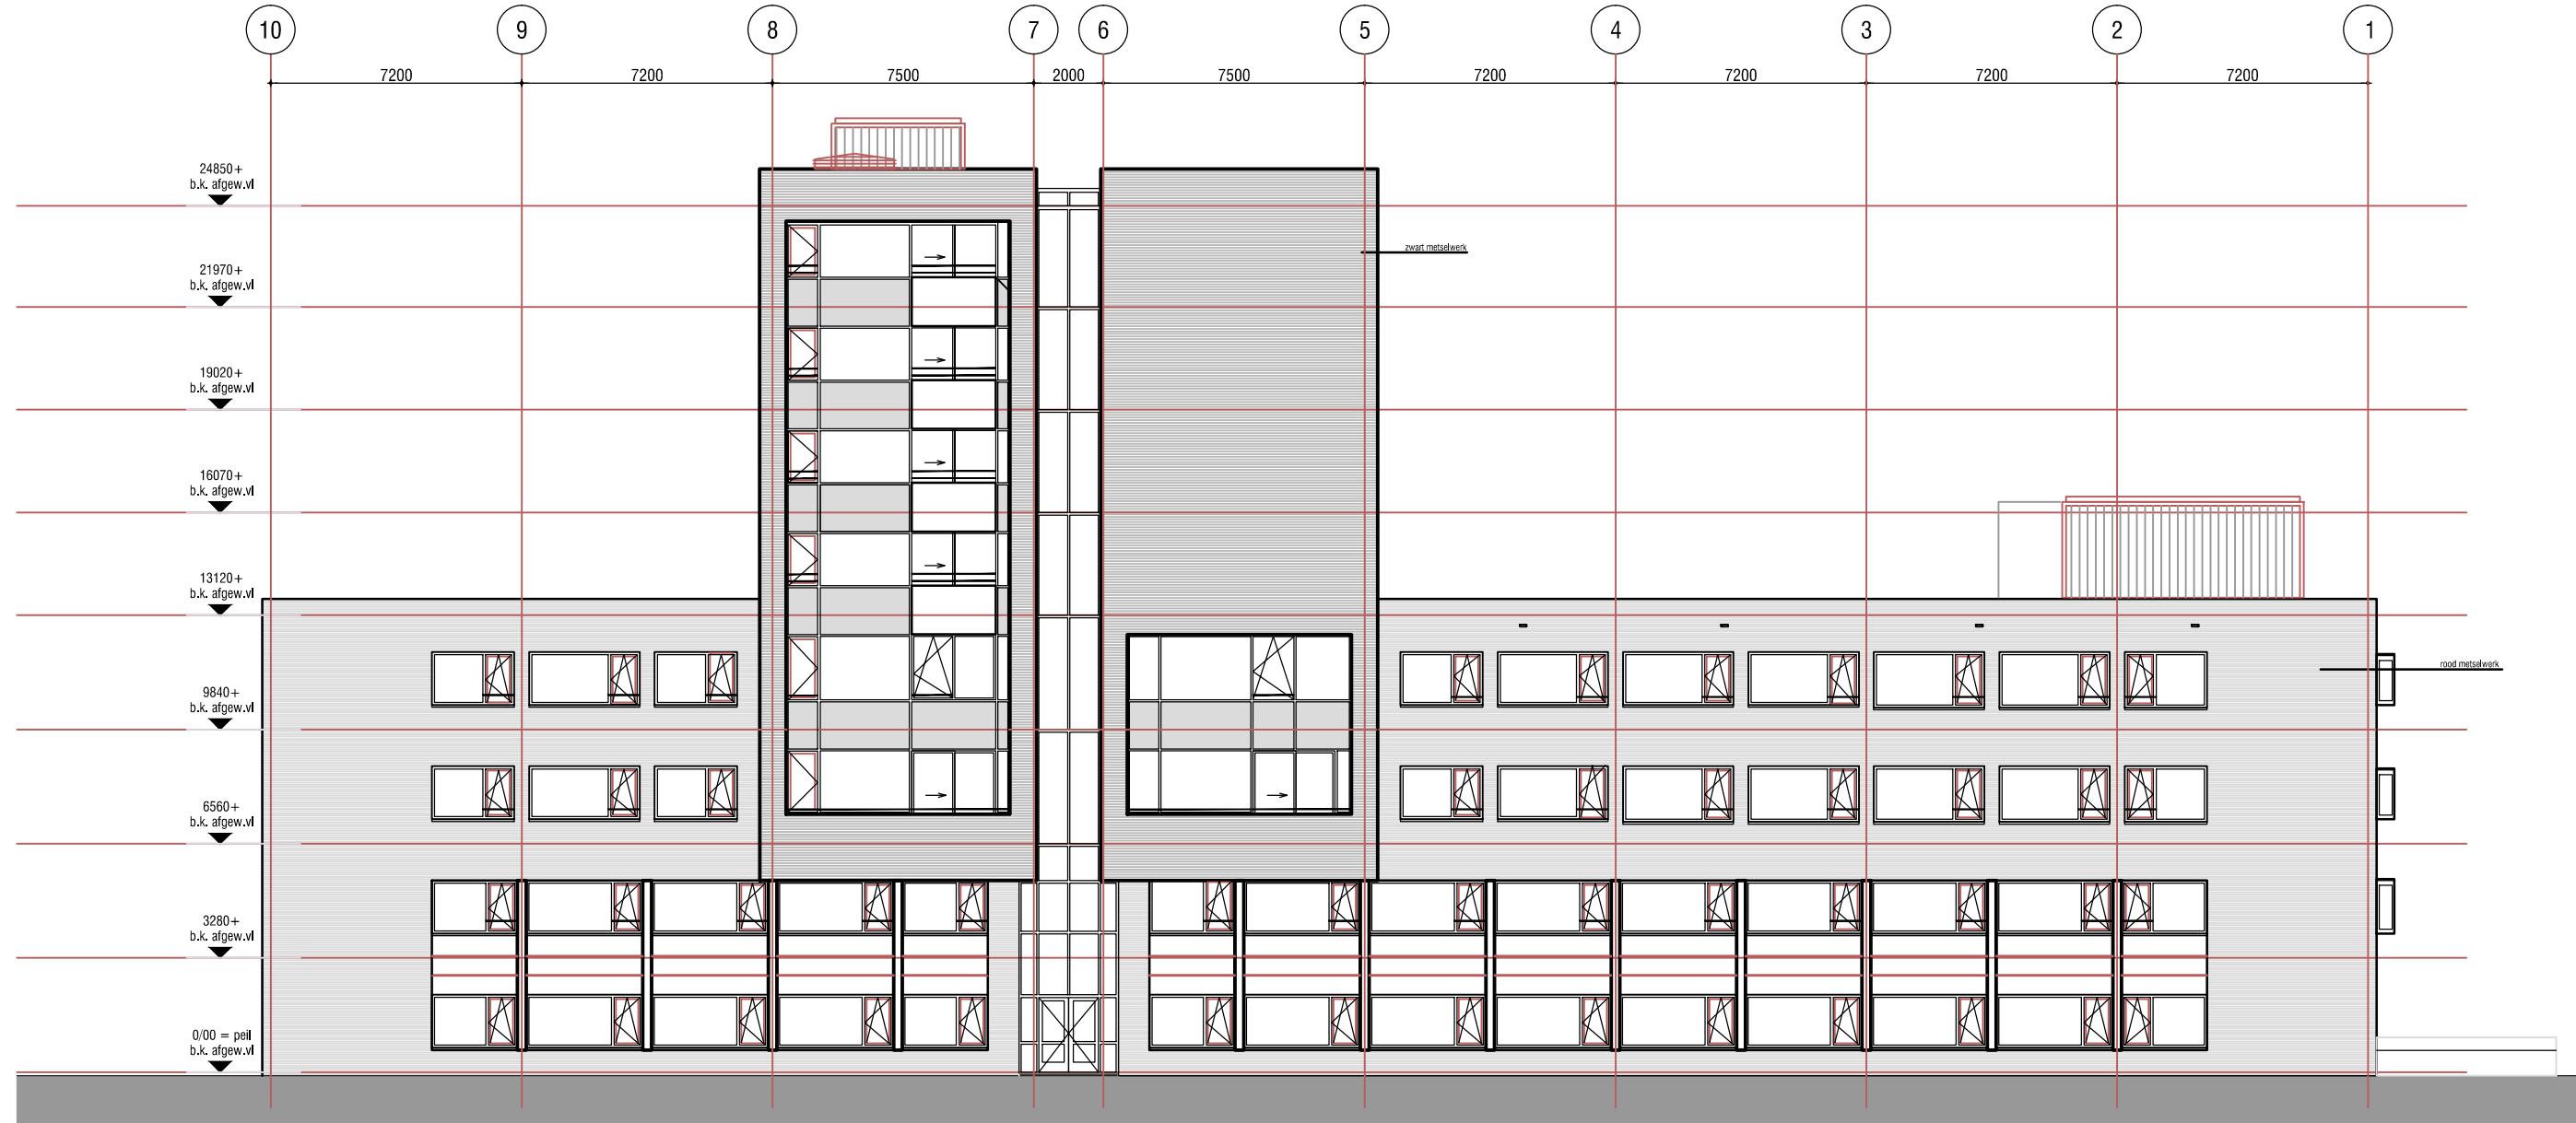


NOORDOOSTGEVEL

Gevelaanzingten		Tek.no.:	7
Schaal:	1 a 200		
Formaat:	A3		
Get.:	mka		
Gew.:	dec 2006		



NOORDWESTGEVEL

Gevelaanzingten		Tek.no.:	8
Schaal:	1 a 200		
Formaat:	A3		
Get.:	mka		
Gew.:	dec 2006		

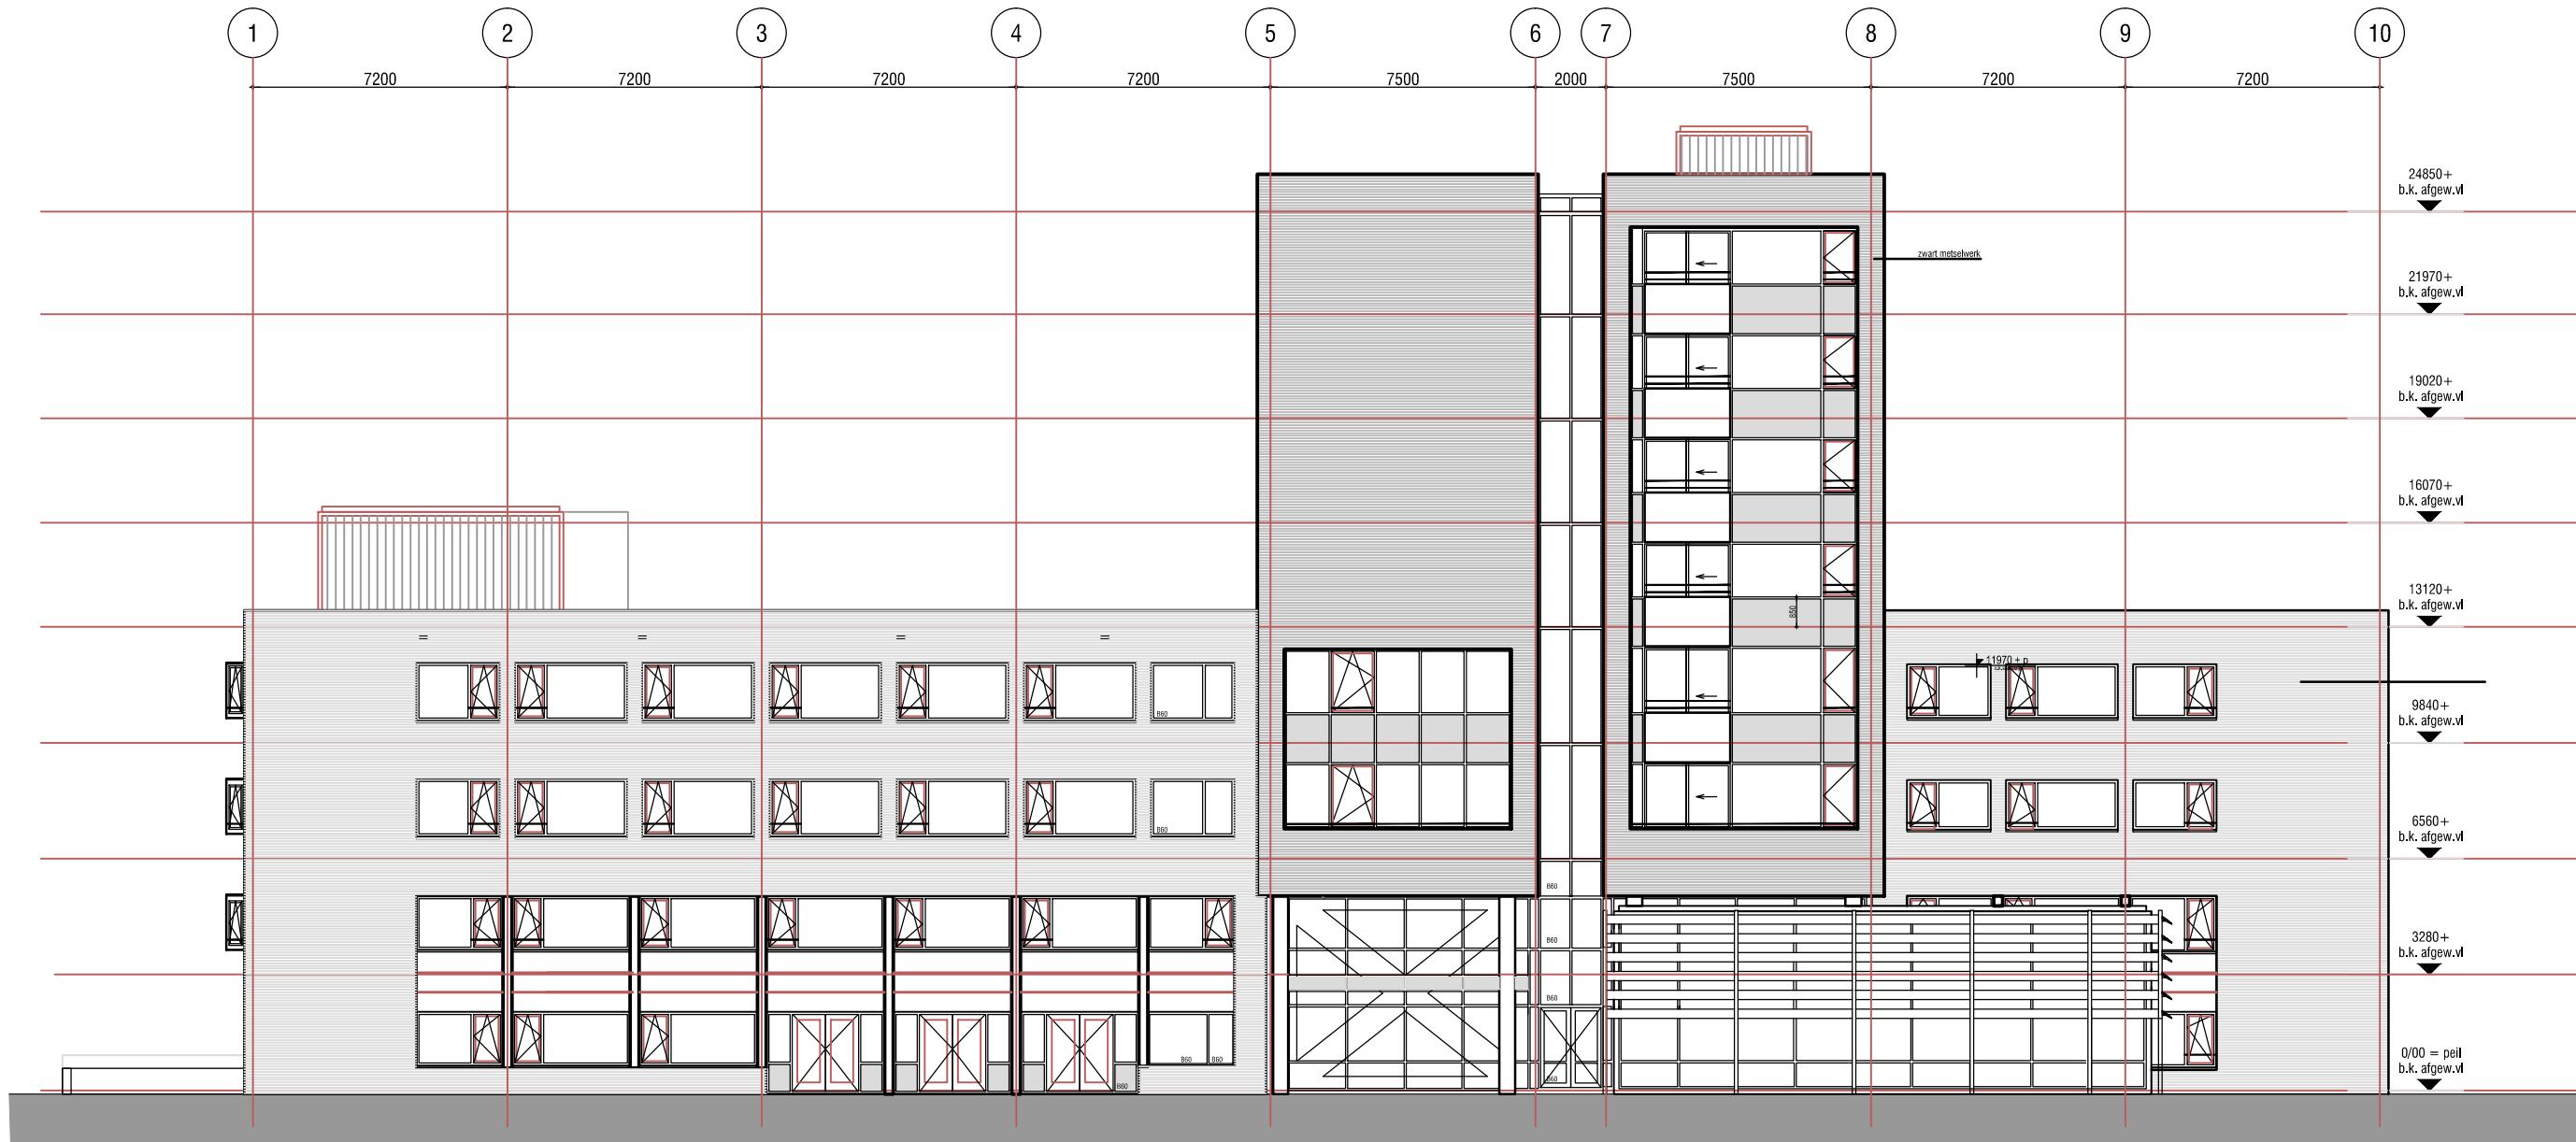


ZUIDWESTGEVEL

Gevelaanzingten		Tek.no.:	9
Schaal:	1 a 200		
Formaat:	A3		
Get.:	mka		
Gew.:	dec 2006		



ZUIDOOSTGEVEL

Doorsnede A - A		Tek.no.:	10
Schaal:	1 a 200		
Formaat:	A3		
Get.:	mka		
Gew.:	dec 2006		

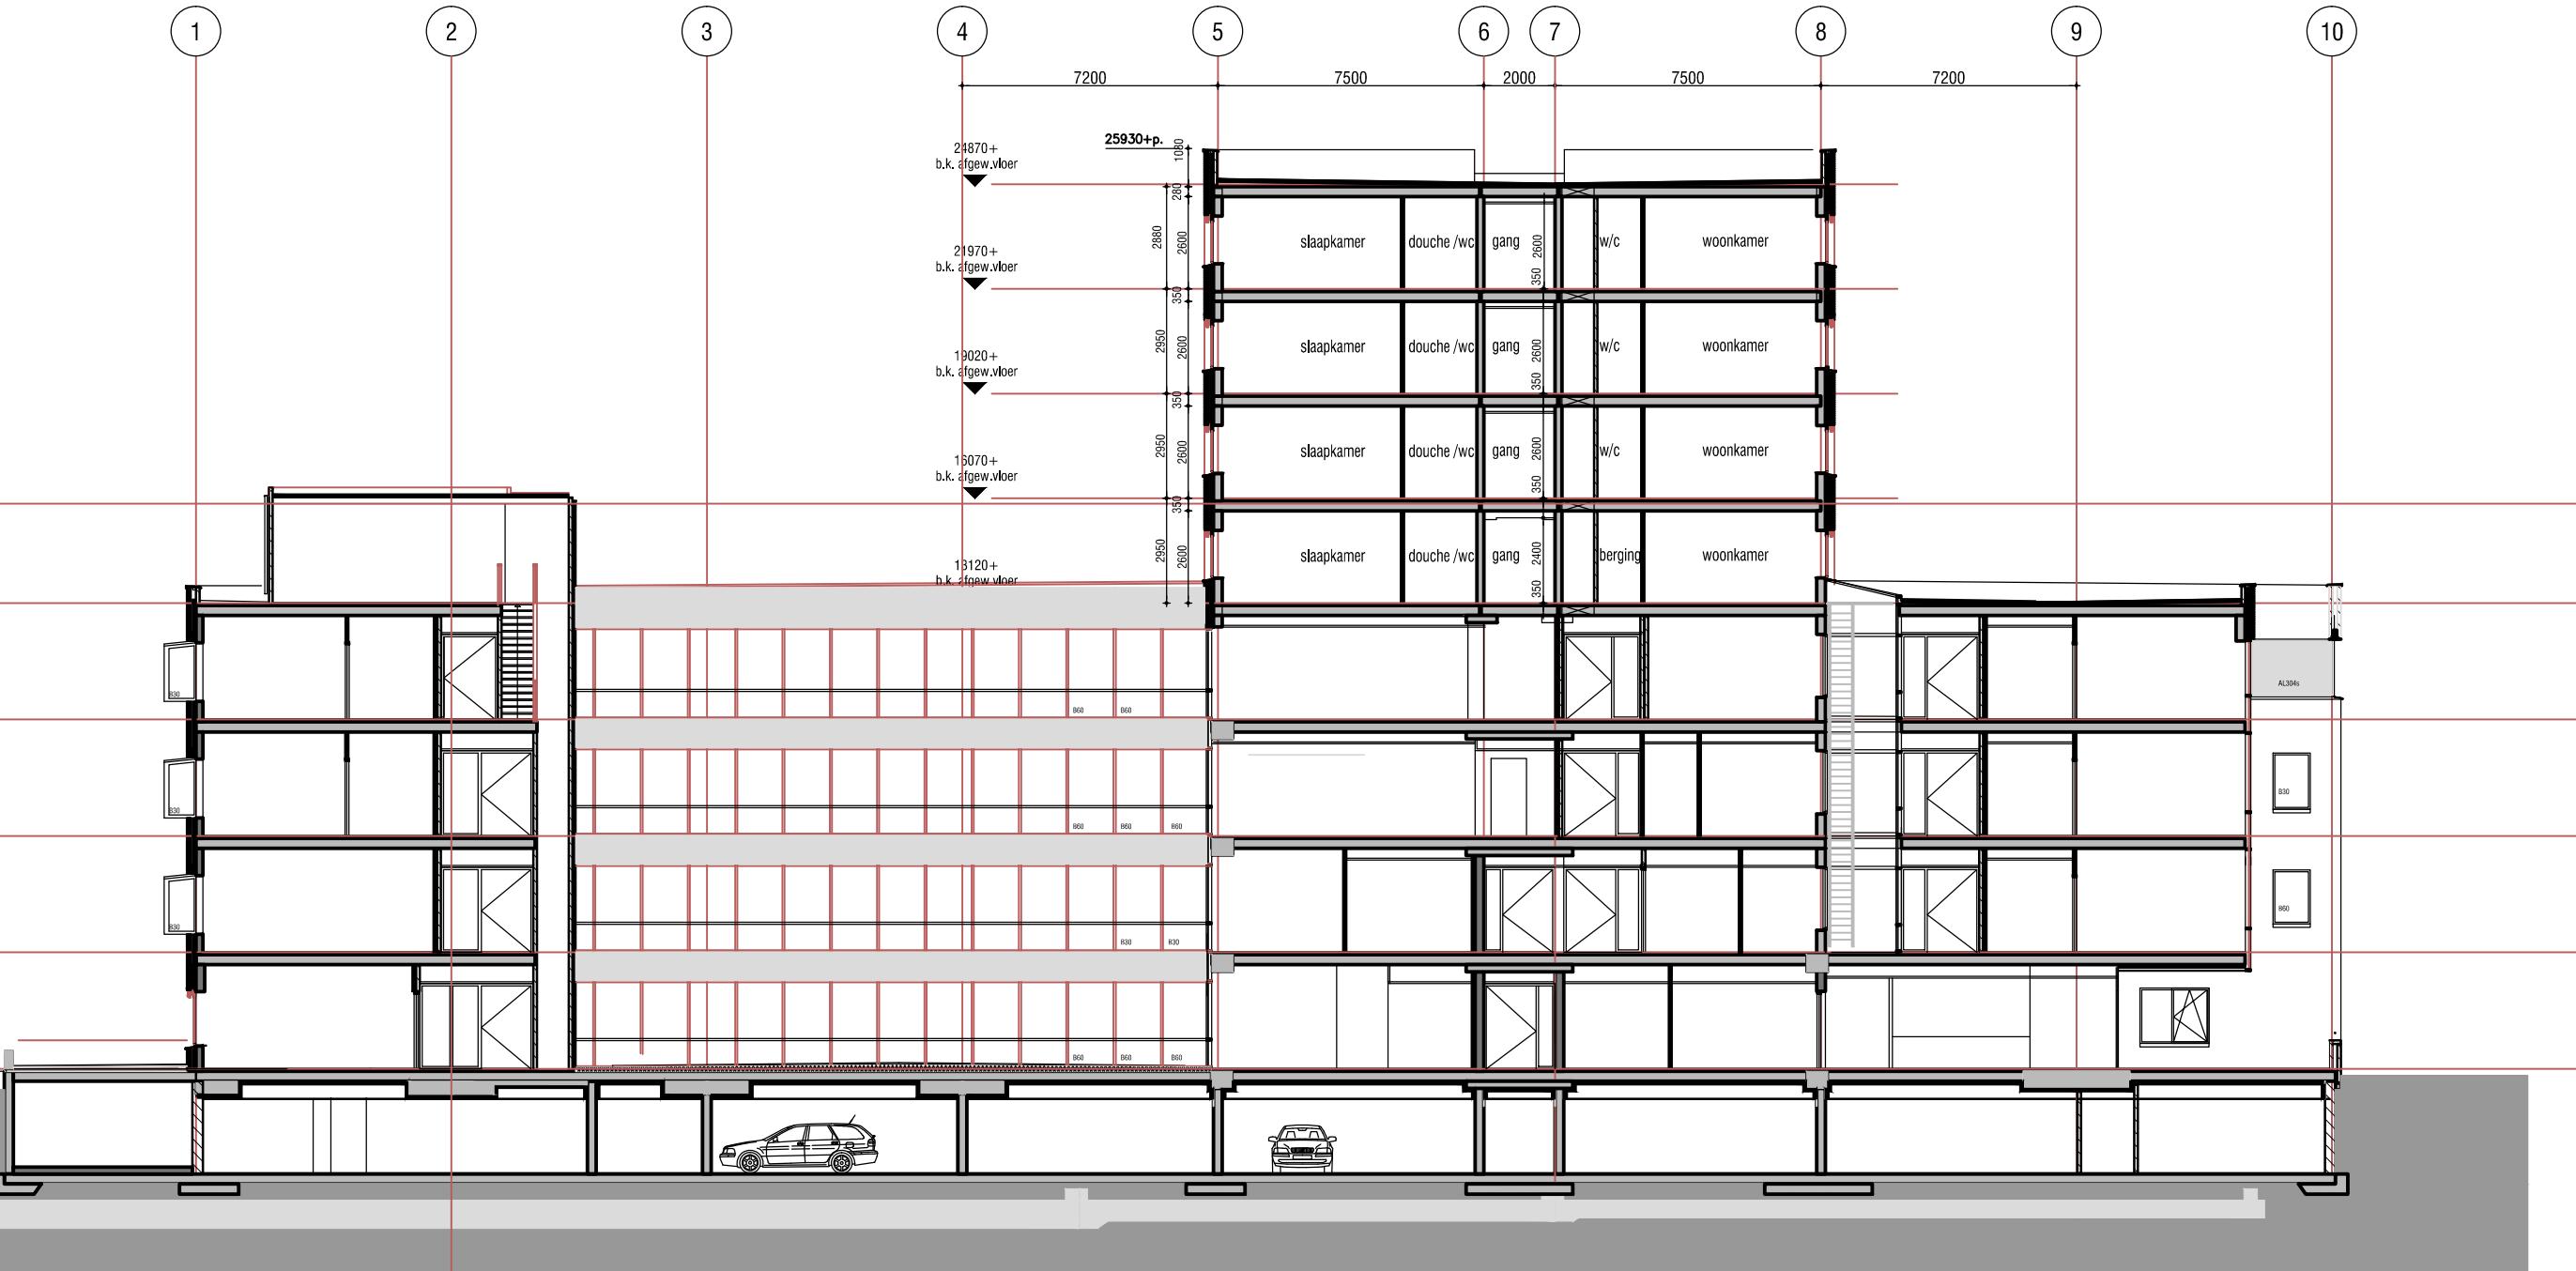

DOORSNEDEN A-A

Doorsnede B - B


Tek.no.: 11

Schaal:	1 a 200
Formaat:	A3
Get.:	mka
Gew.:	dec 2006



DOORSNEDE B - B


Appartement type 1 - huisnummers 6, 20, 36 en 52		Tek.no.:	12
Schaal:	1 a 50		
Formaat:	A3		
Géf.:	mka		
Gew.:	dec 2006		

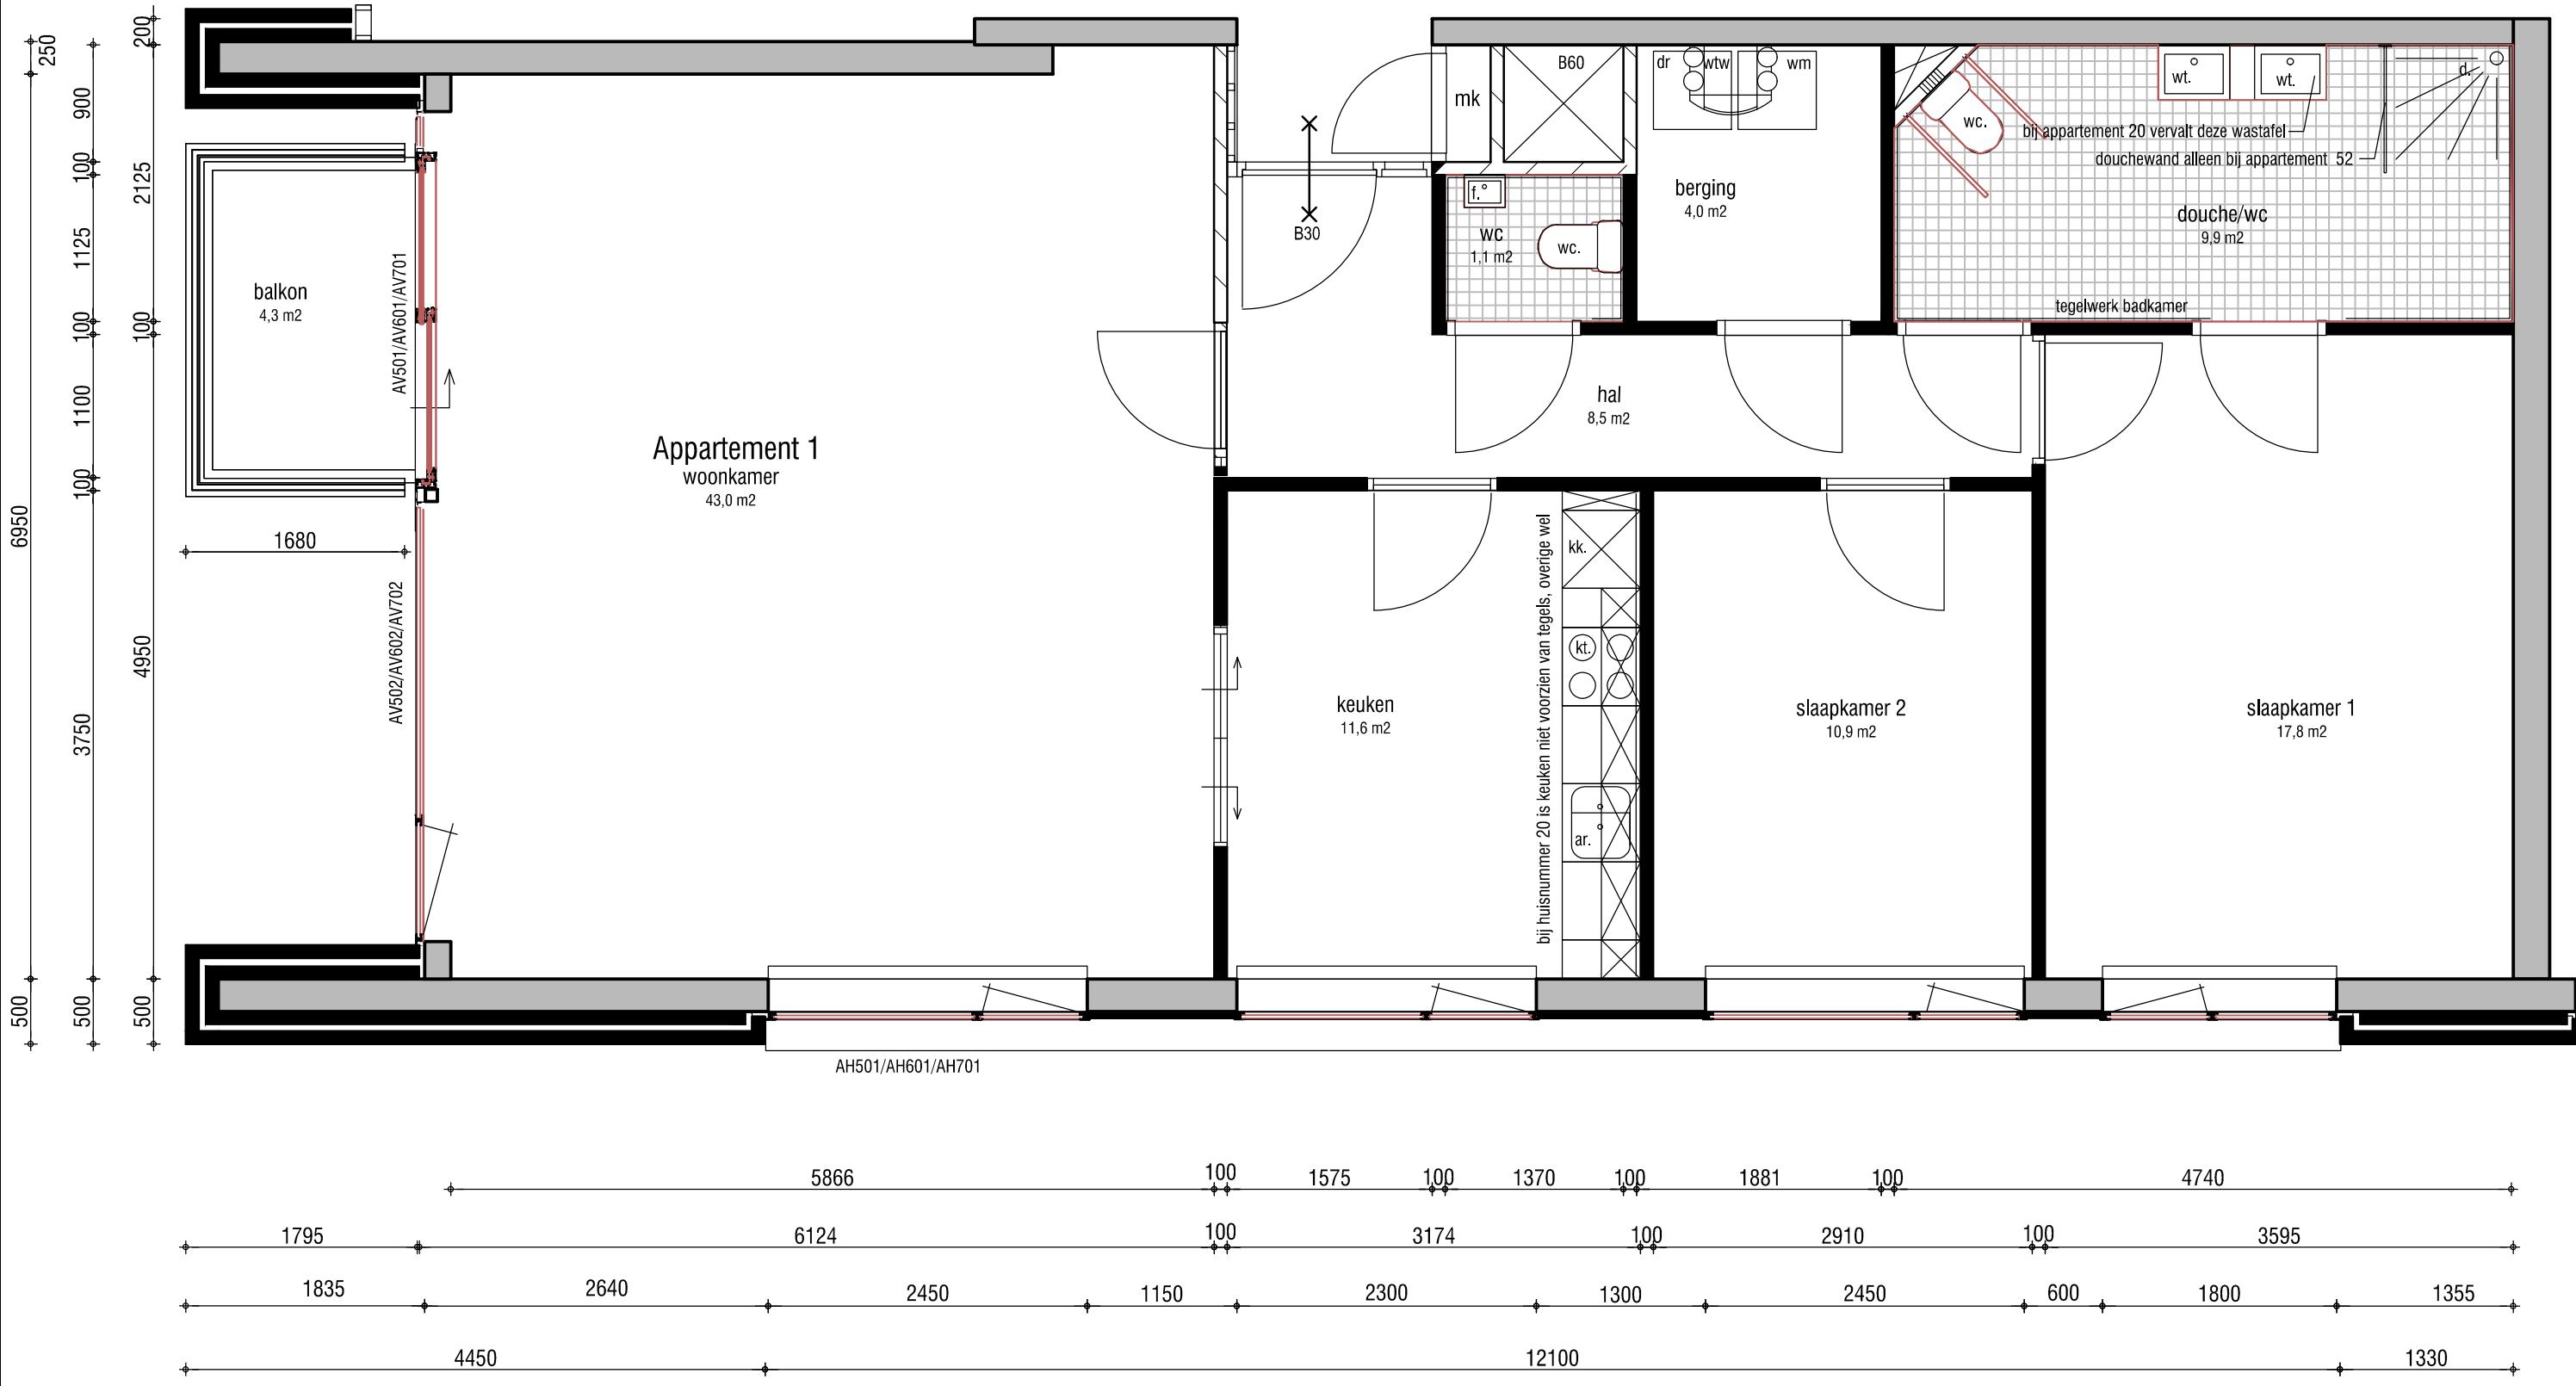


Appartement type 2 - huisnummers 34, 50 en 66

Tek.no.:

13

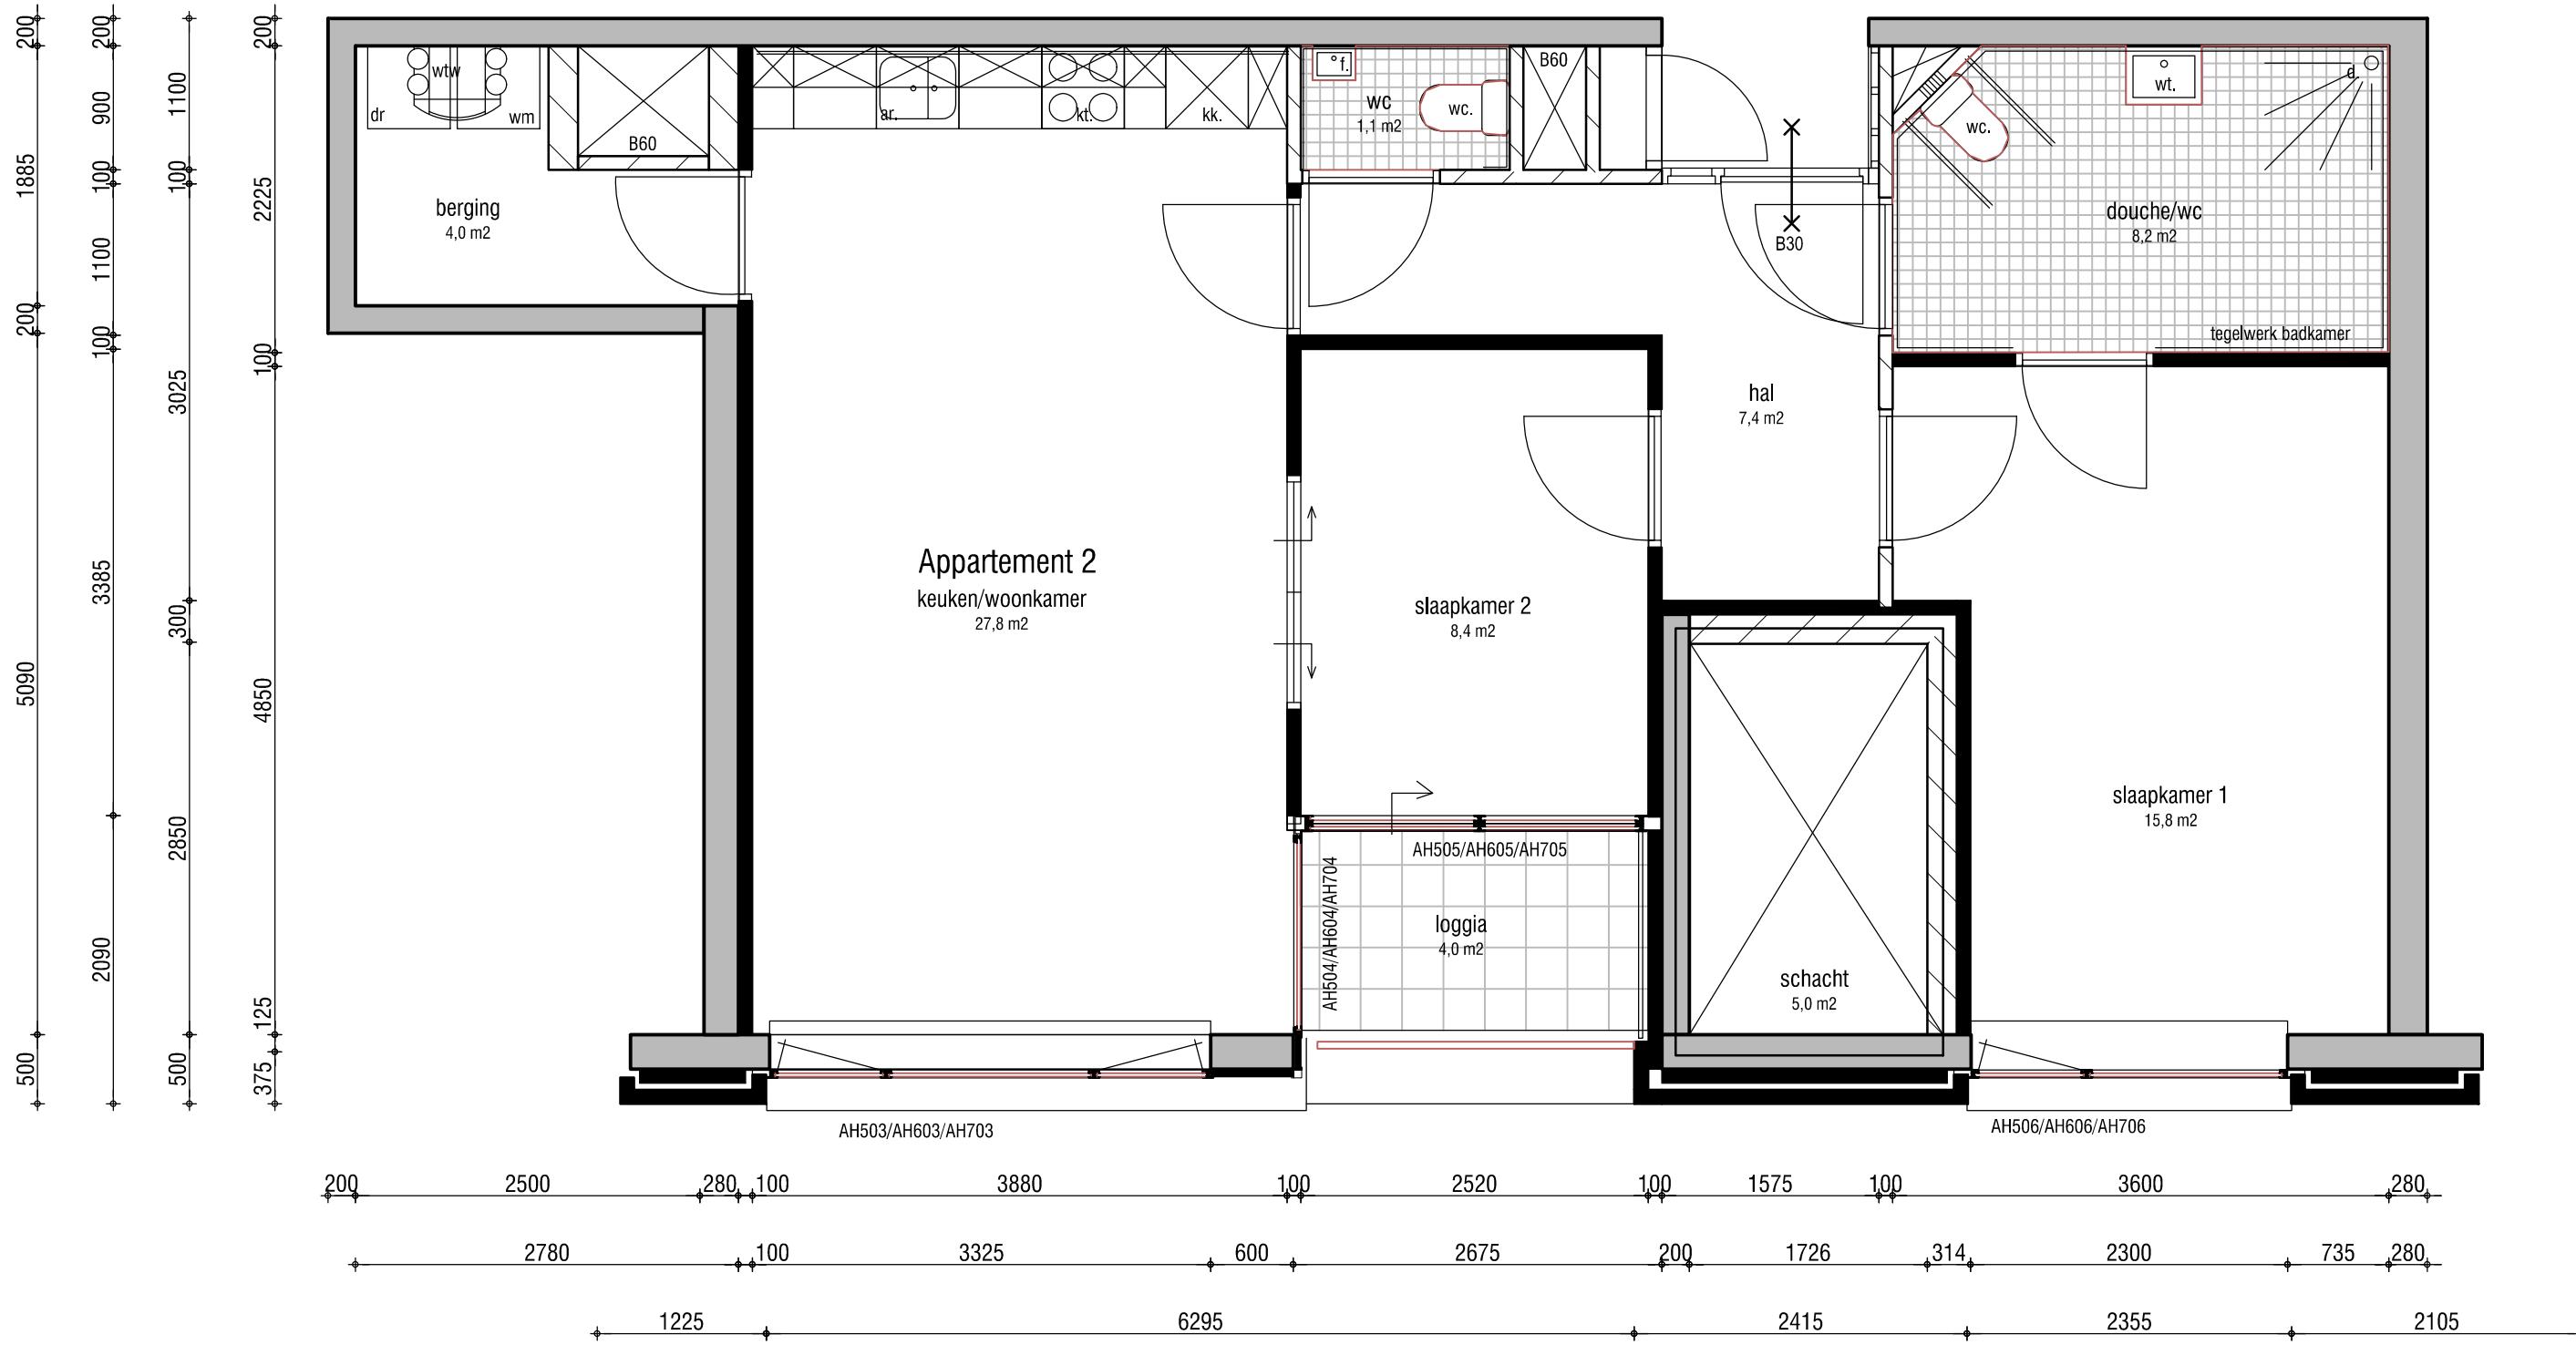


Appartement type 3 - huisnummers 32, 48 en 64		Tek.no.:	15
Schaal:	1 a 50		
Formaat:	A3		
Get.:	mka		
Gew.:	dec 2006		

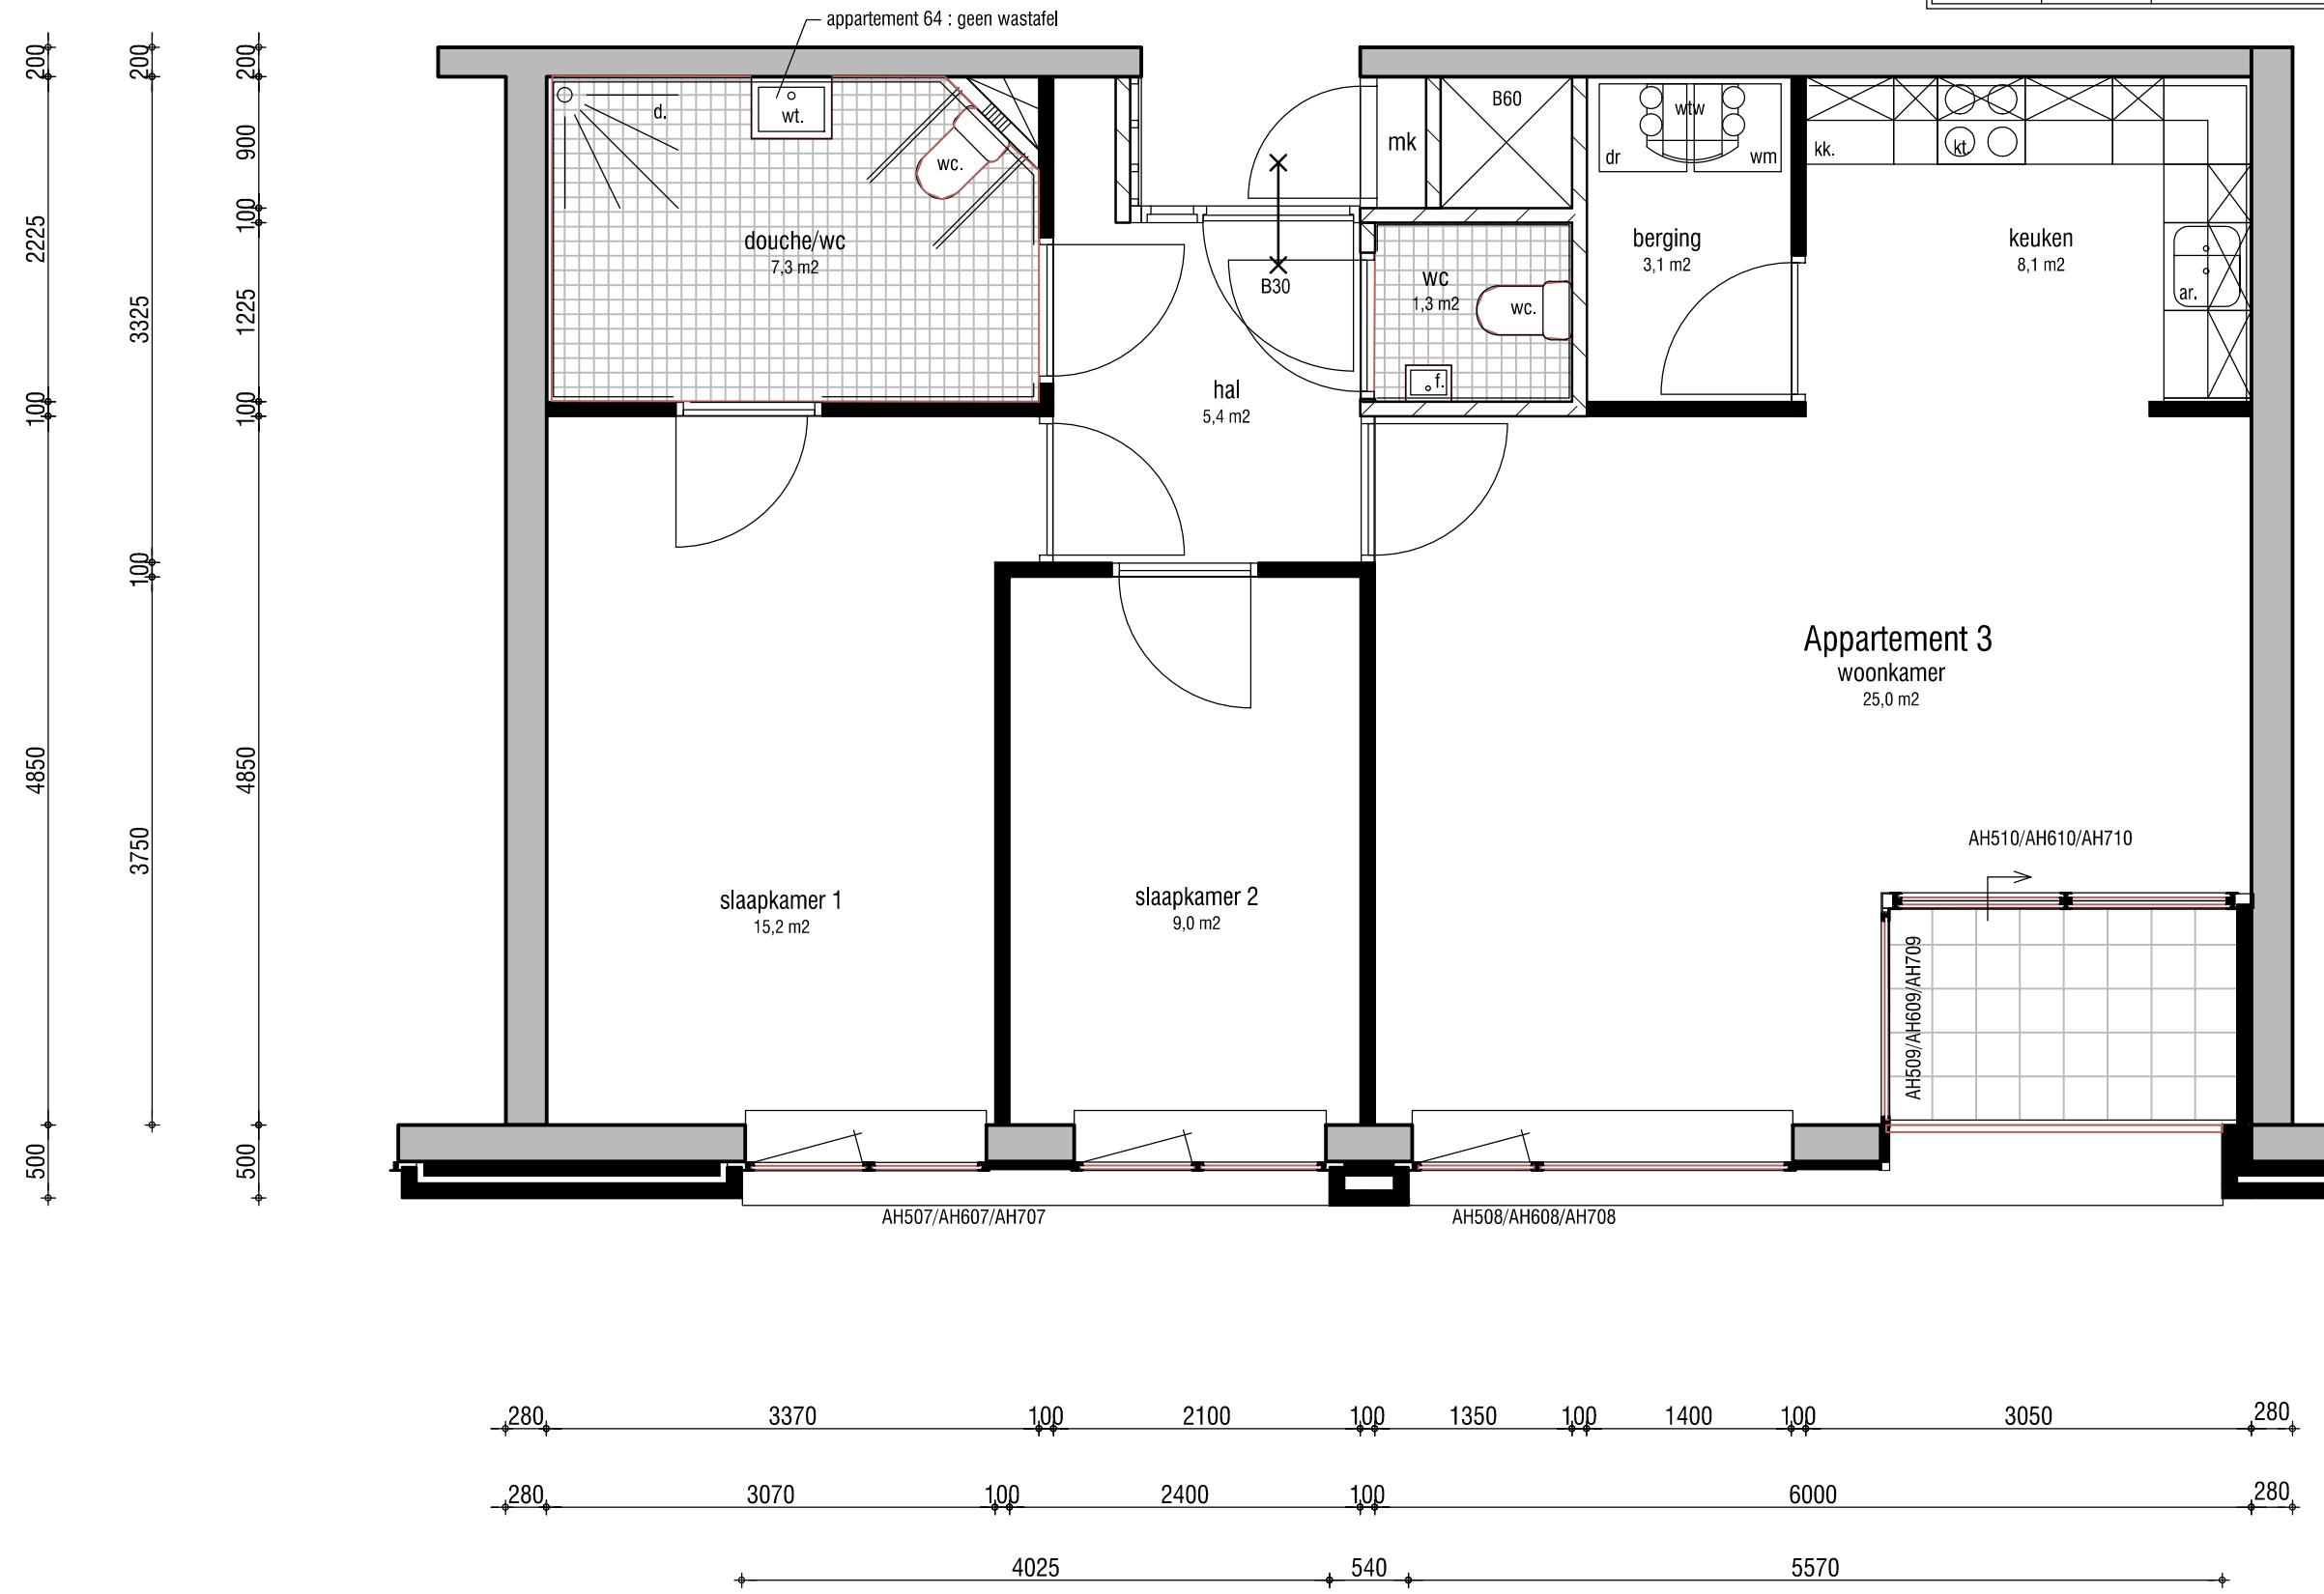

Appartement type 3a - huisnummer 18


Tek.no.: 14

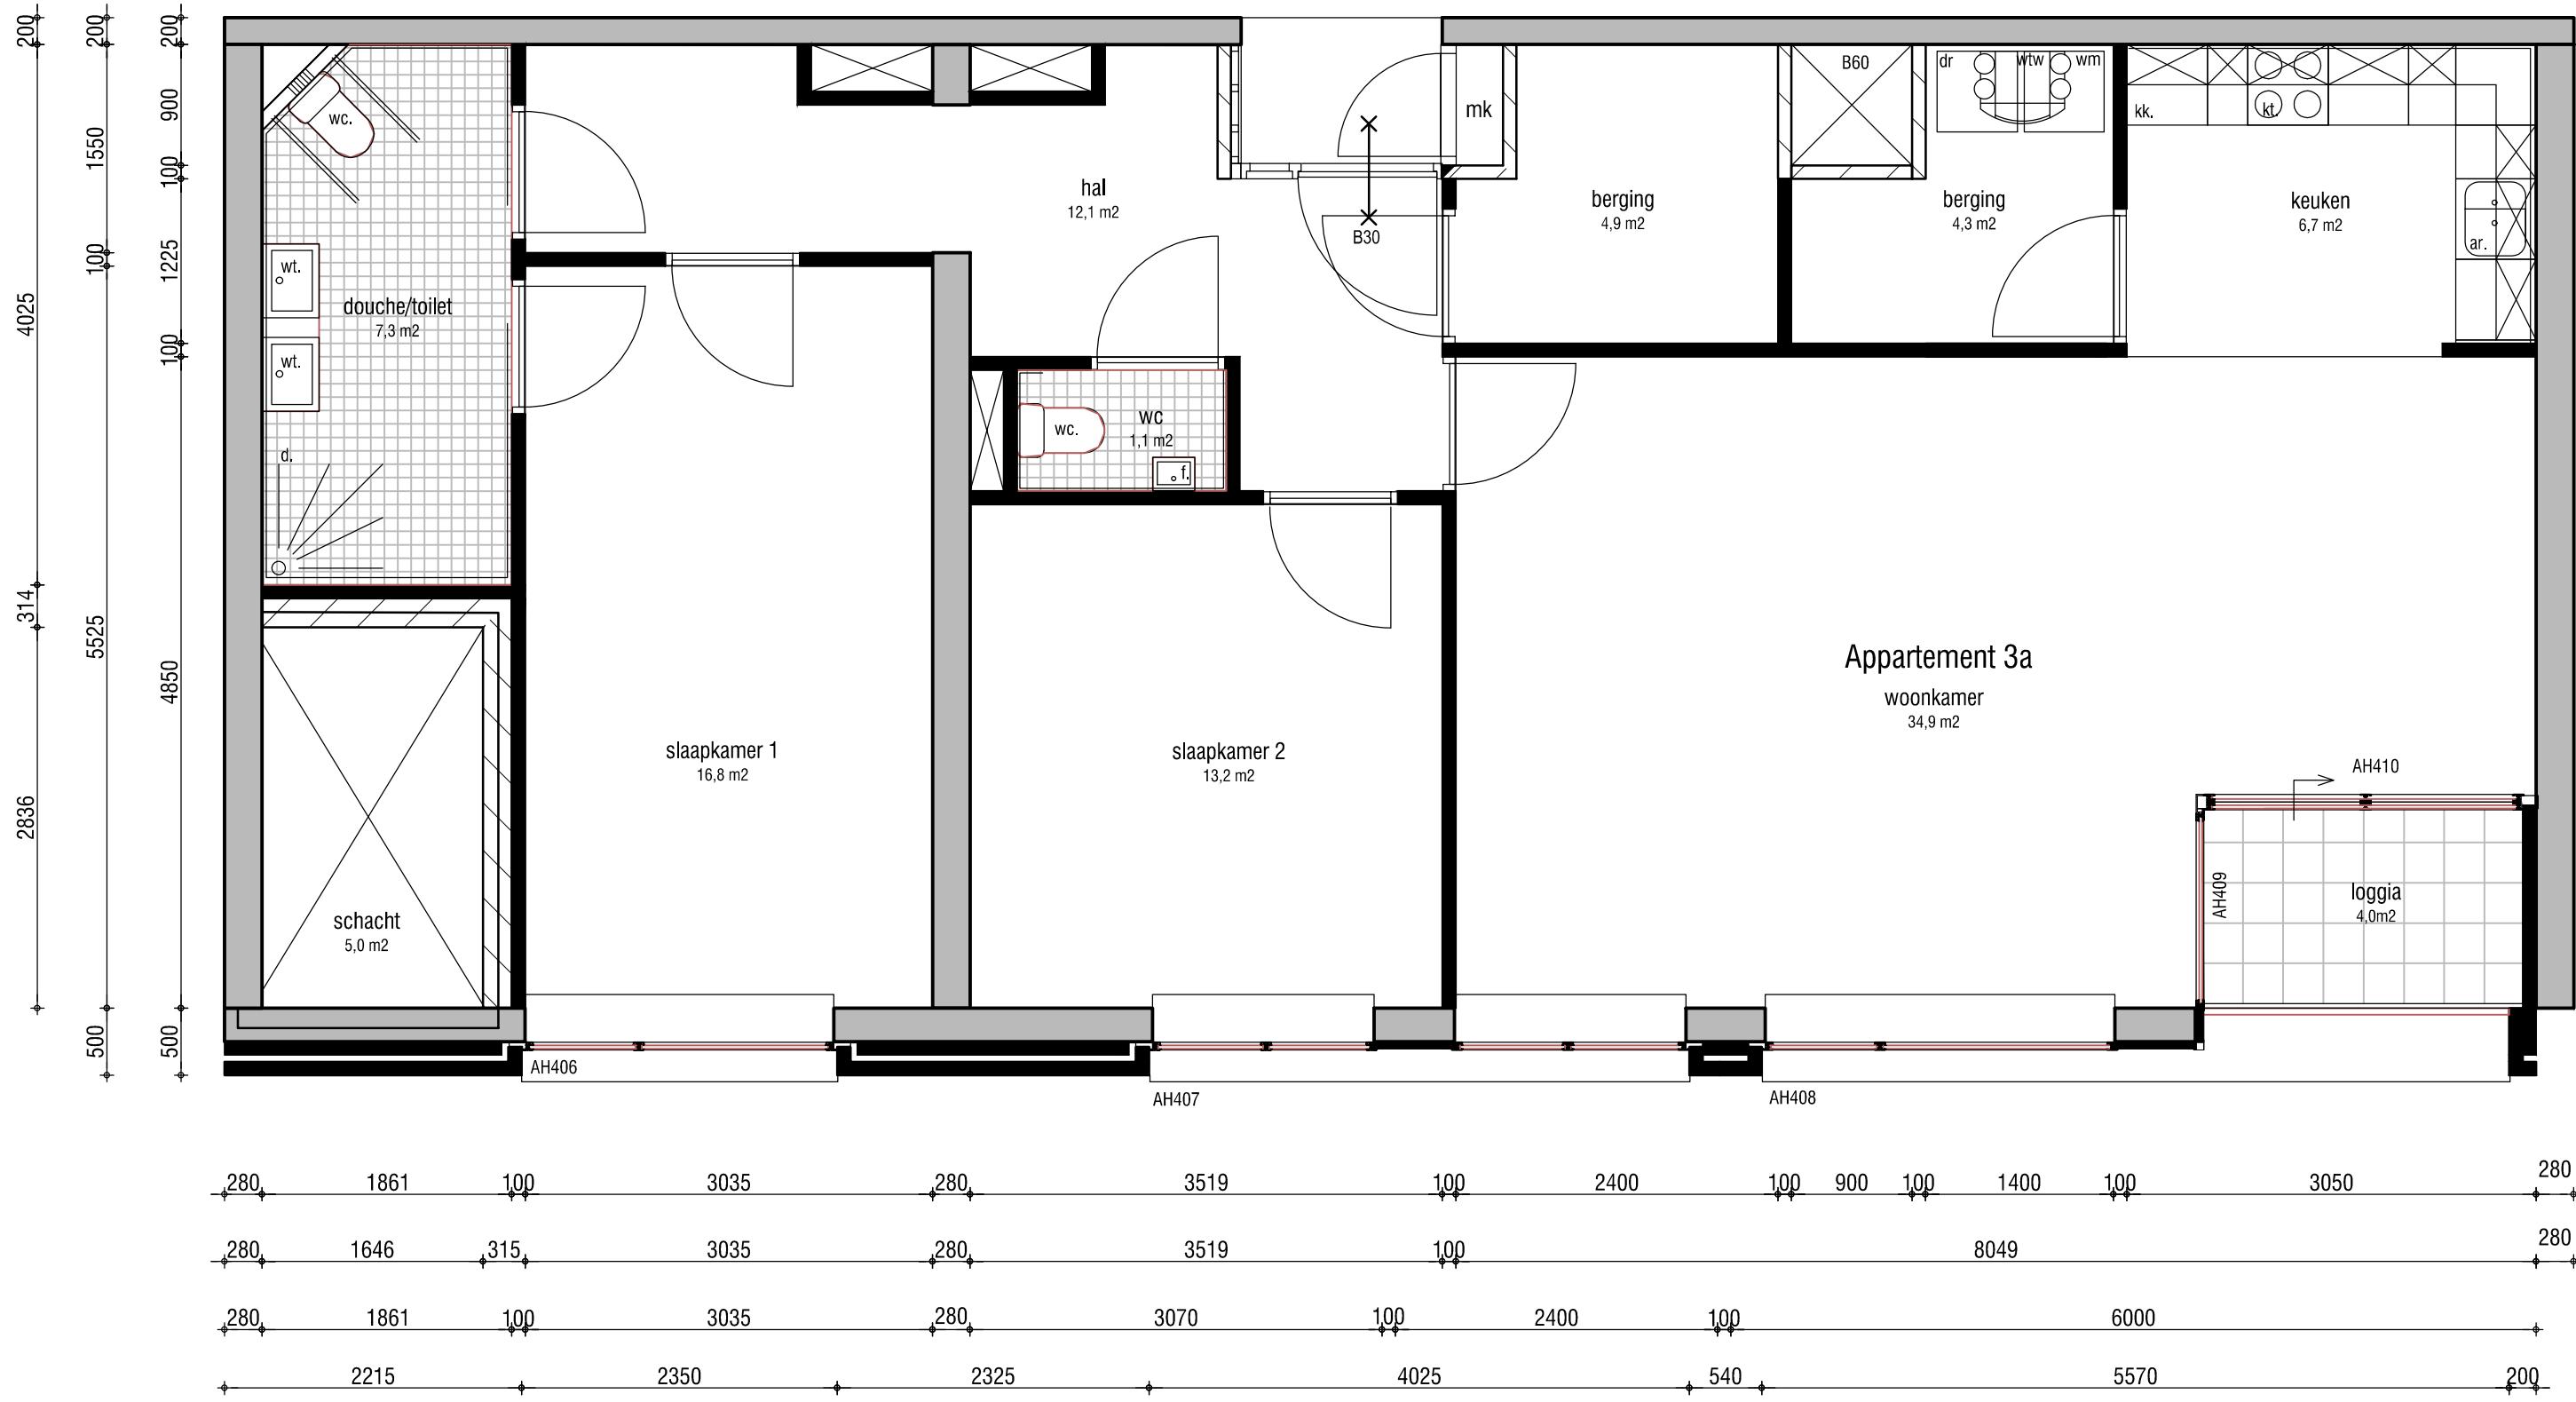


Appartement type 4 - huisnummers 16, 30, 46 en 62 Tek.no.: 16


Schaal:	1 a 50
Formaat:	A3
Get.:	mka
Gew.:	dec 2006

 


Appartement type 5 - huisnummers 14, 28, 44 en 60		Tek.no.:	17
Schaal:	1 a 50		
Formaat:	A3		
Get.:	mka		
Gew.:	dec 2006		

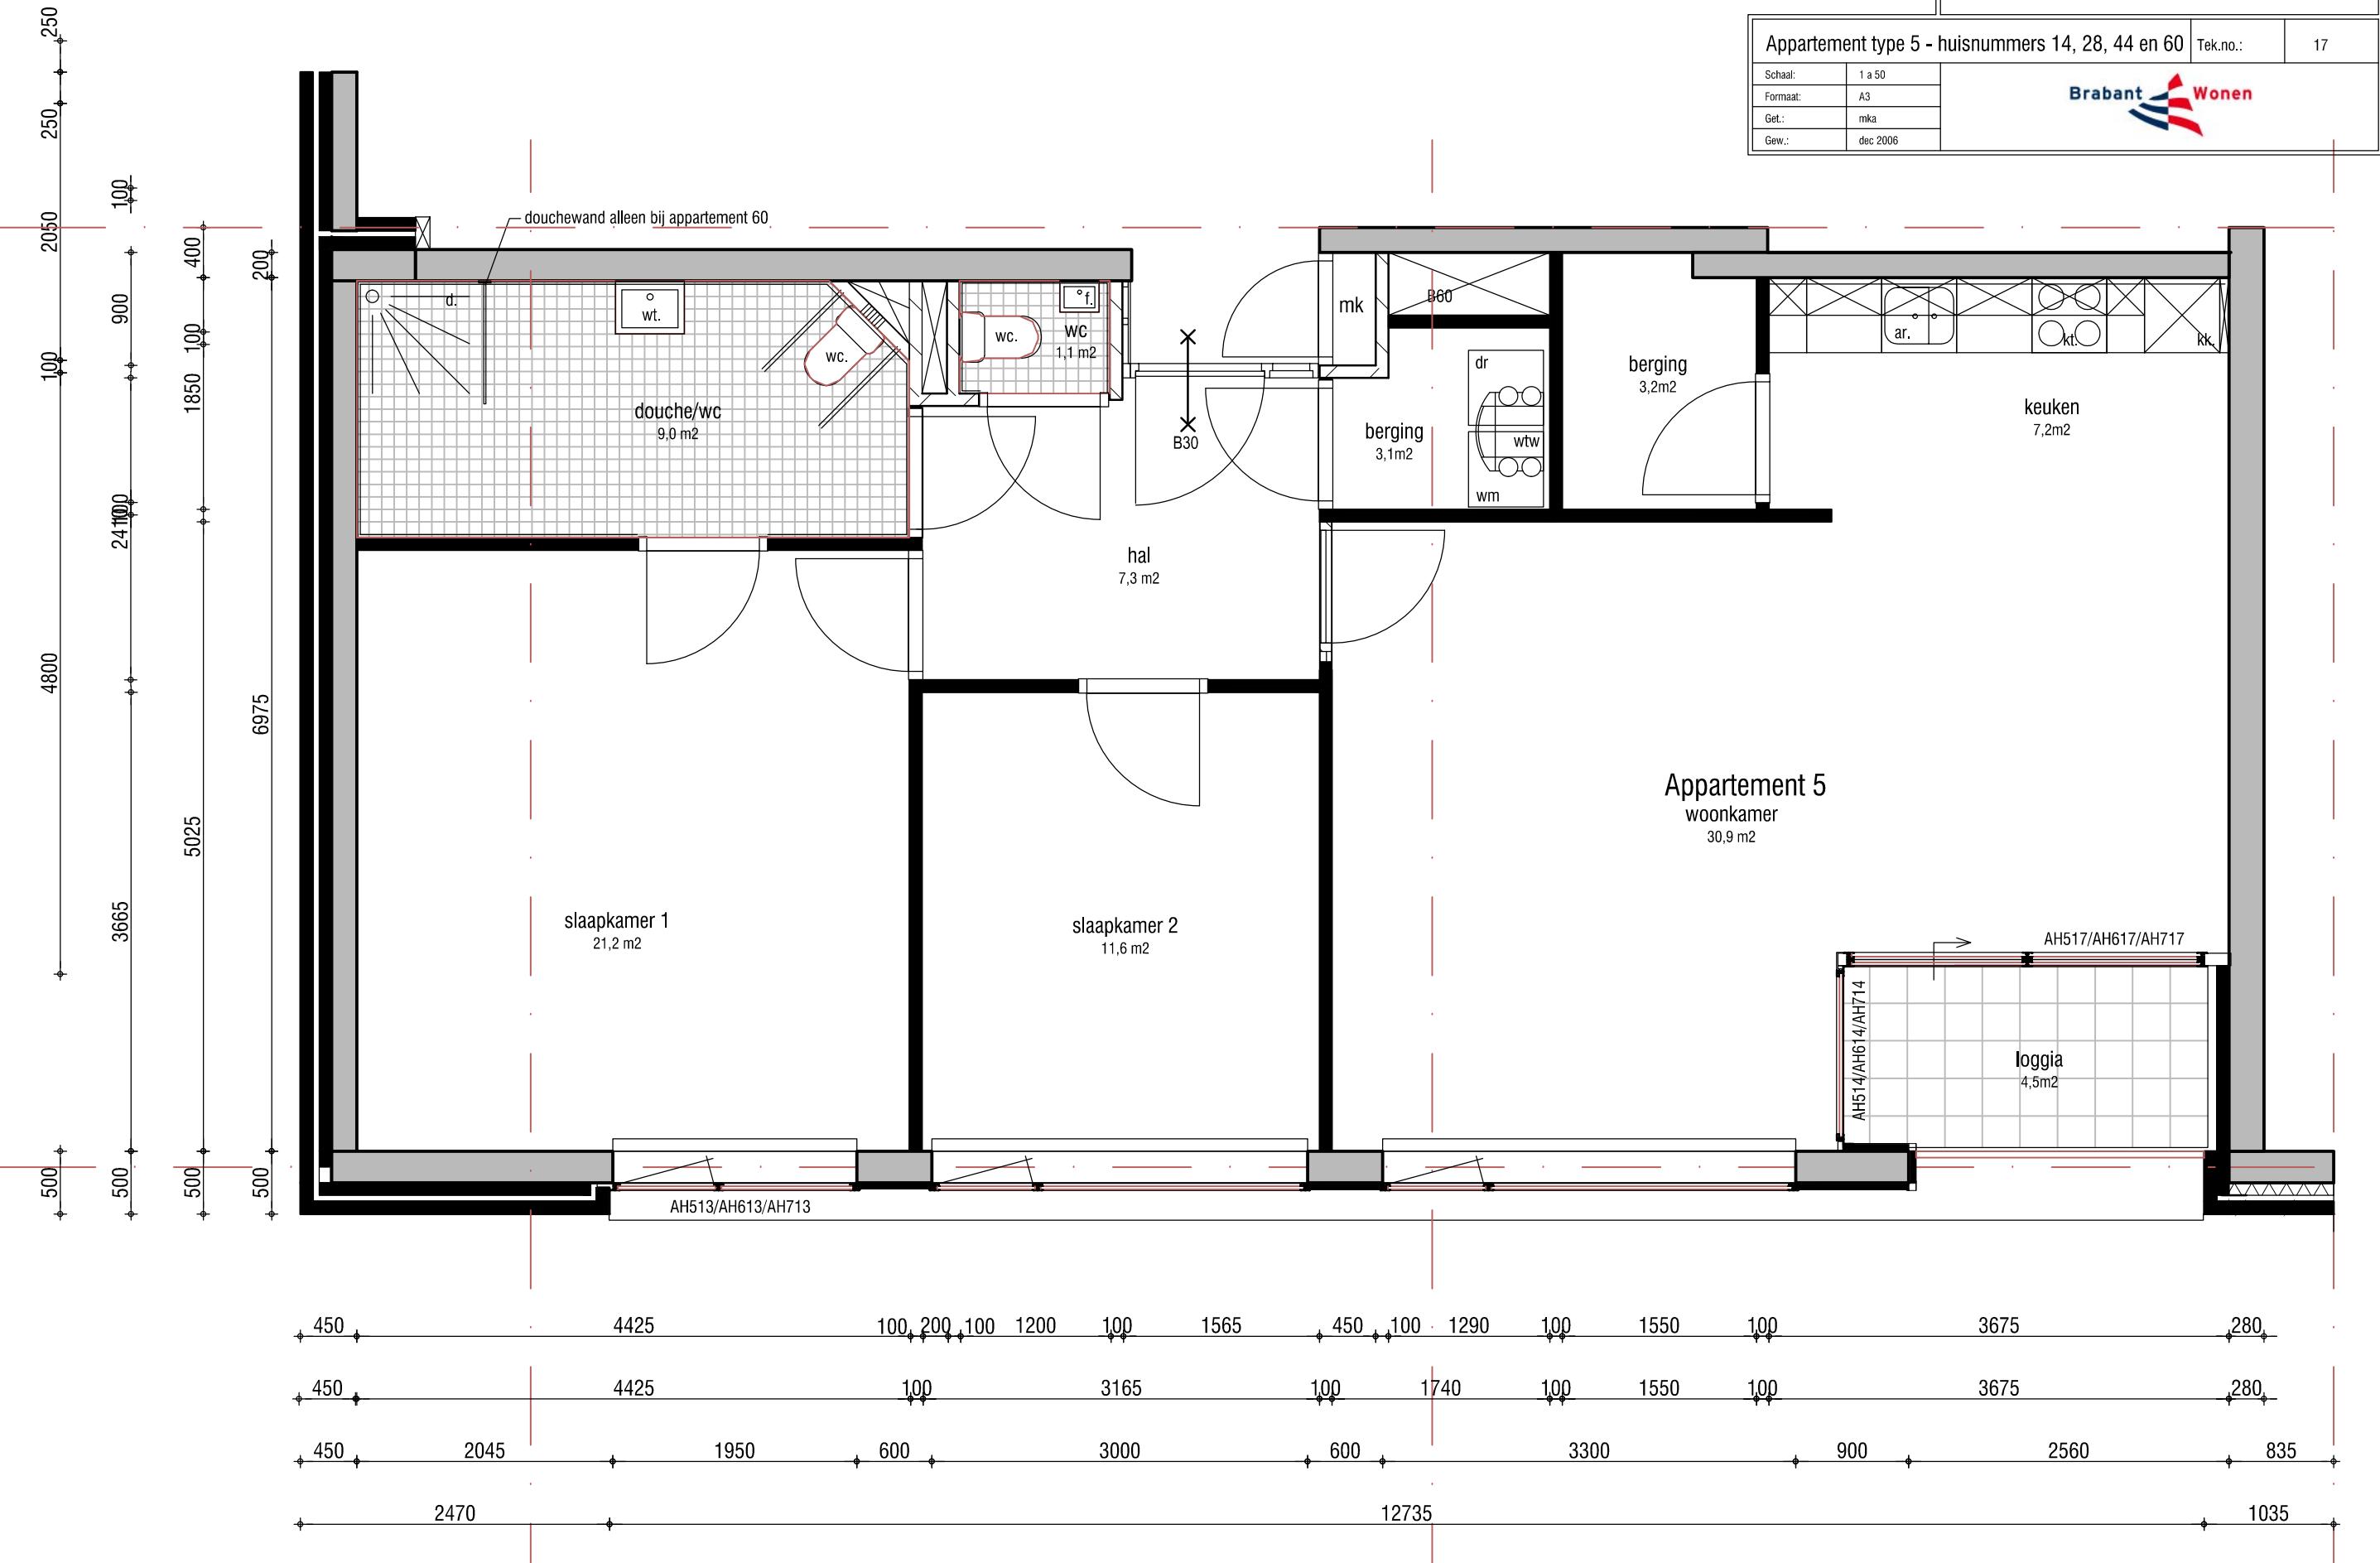

Appartement type 6 - huisnummers 12, 26, 42 en 58		Tek.no.:	18
Schaal:	1 a 50		
Formaat:	A3		
Gel.:	mka		
Gew.:	dec 2006		

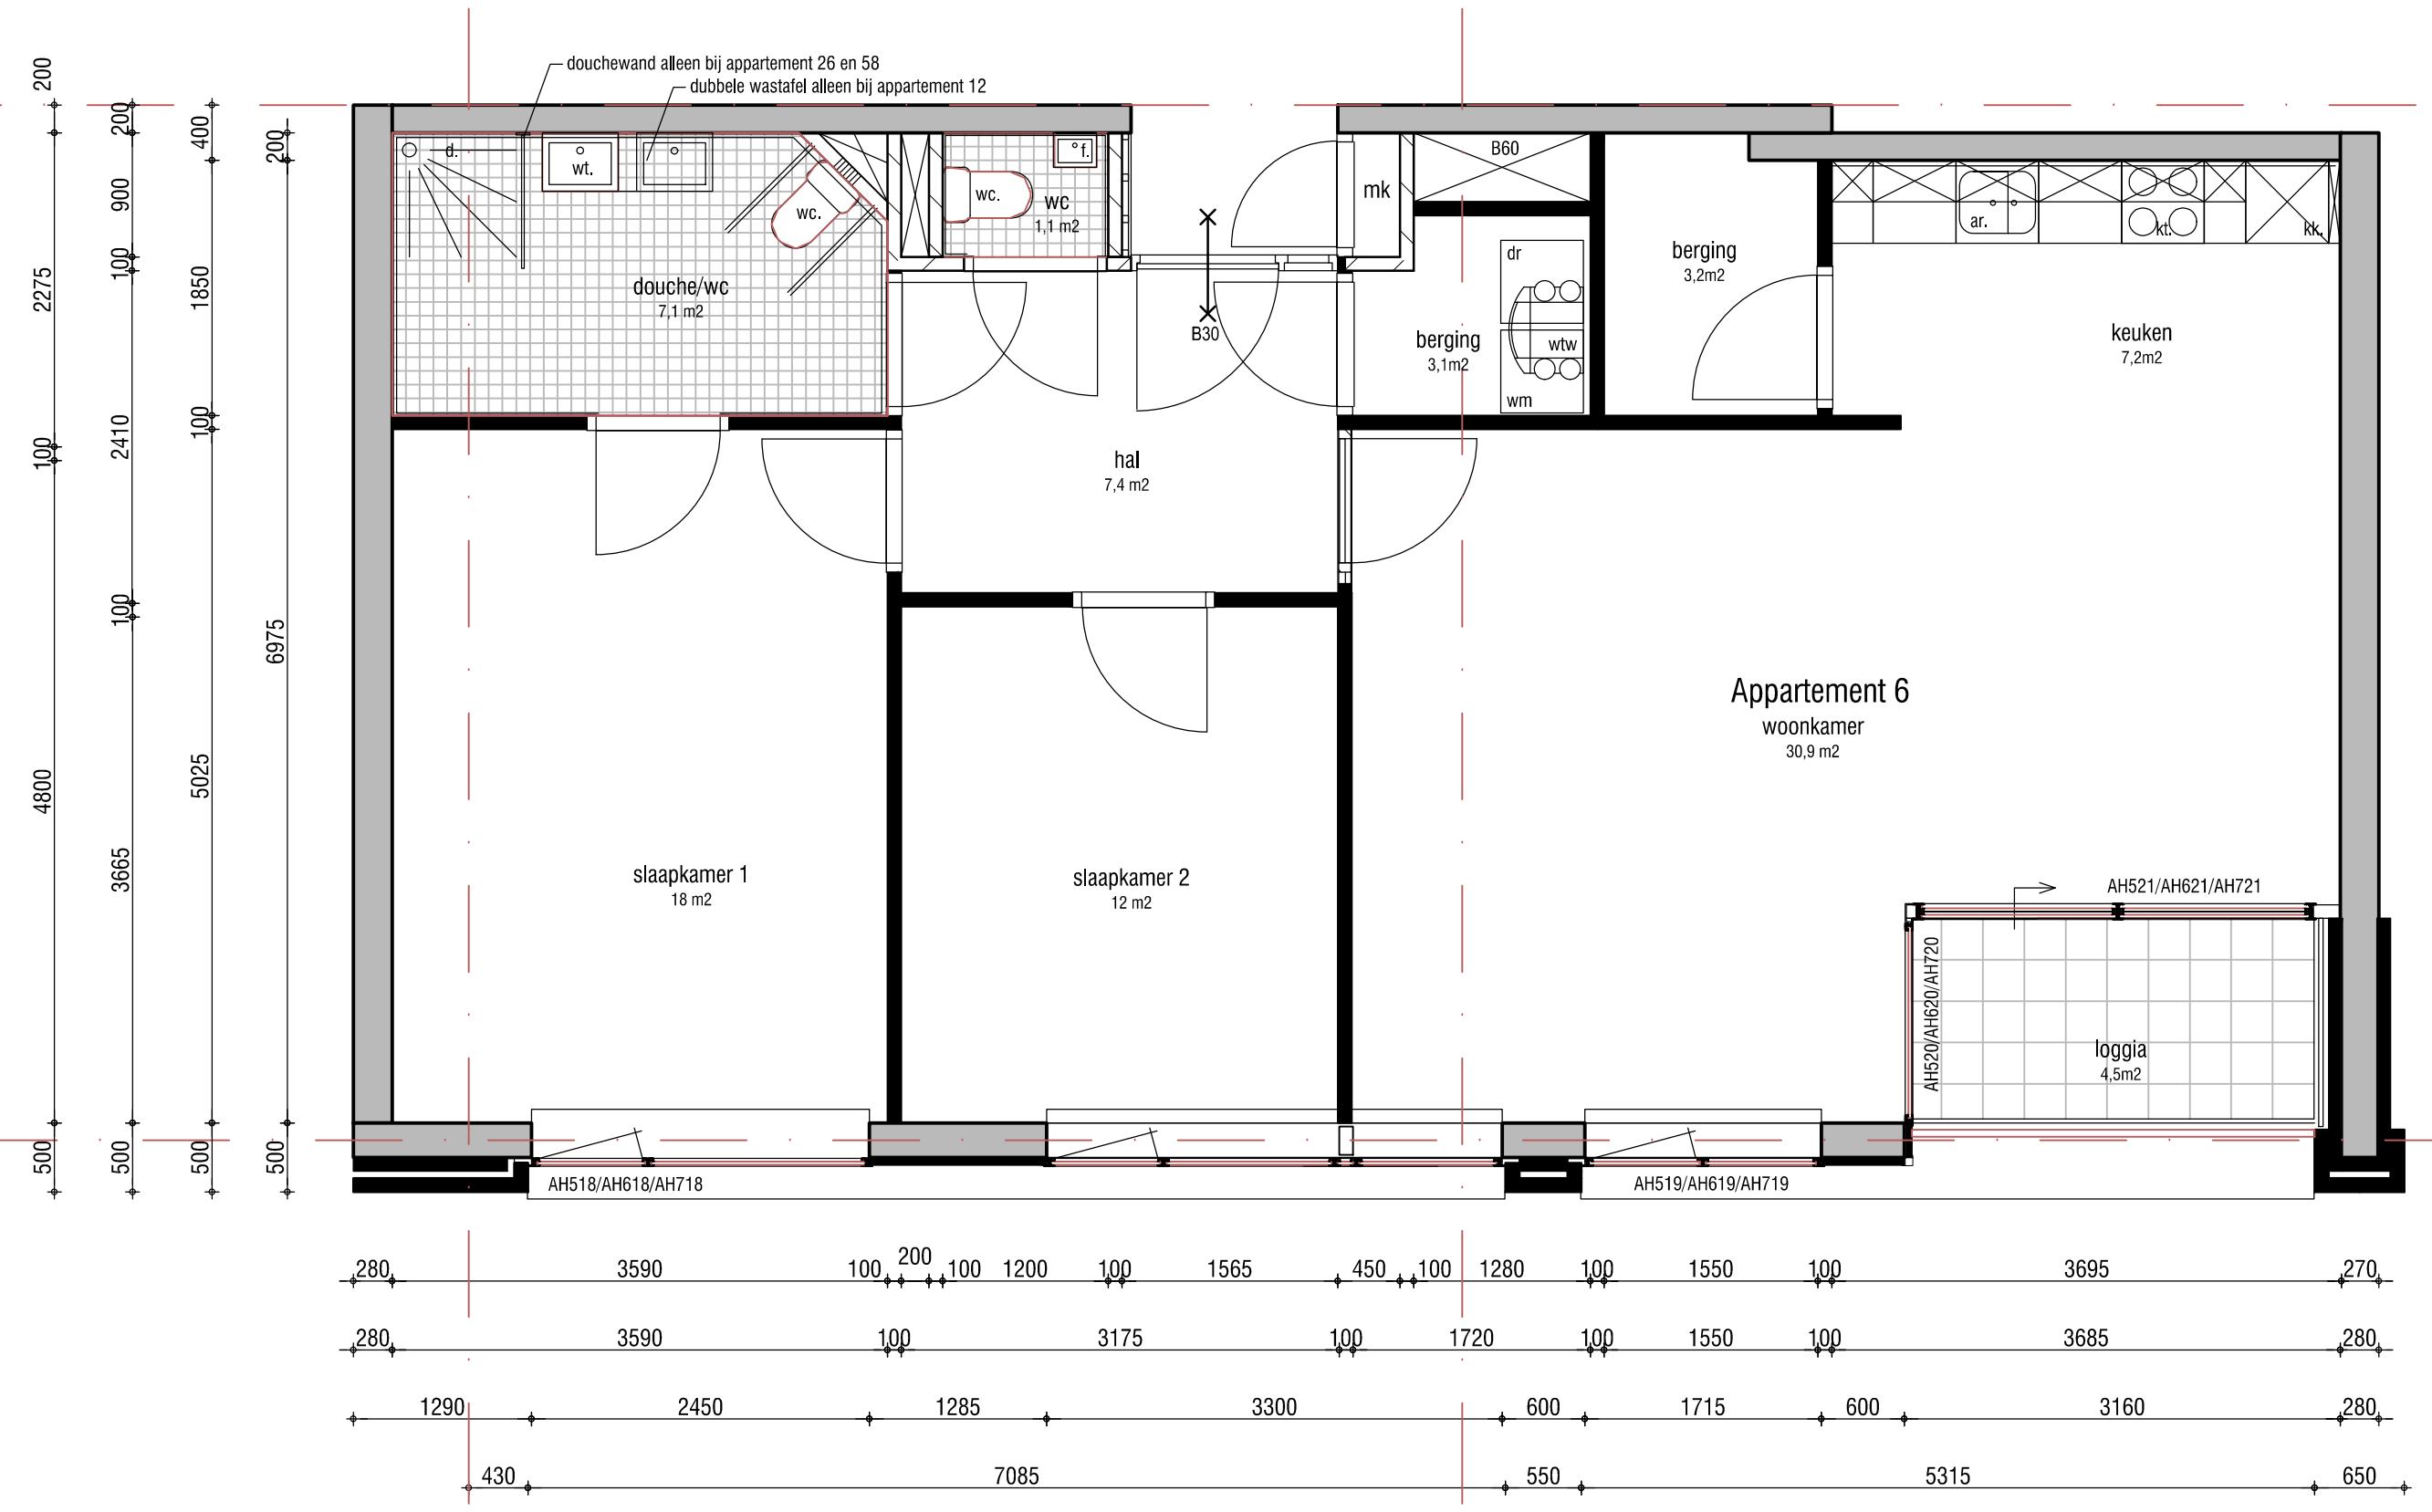

Appartement type 7 - huisnummers 10, 24, 40 en 56		Tek.no.:	19
Schaal:	1 a 50		
Formaat:	A3		
Get.:	mka		
Gew.:	dec 2006		

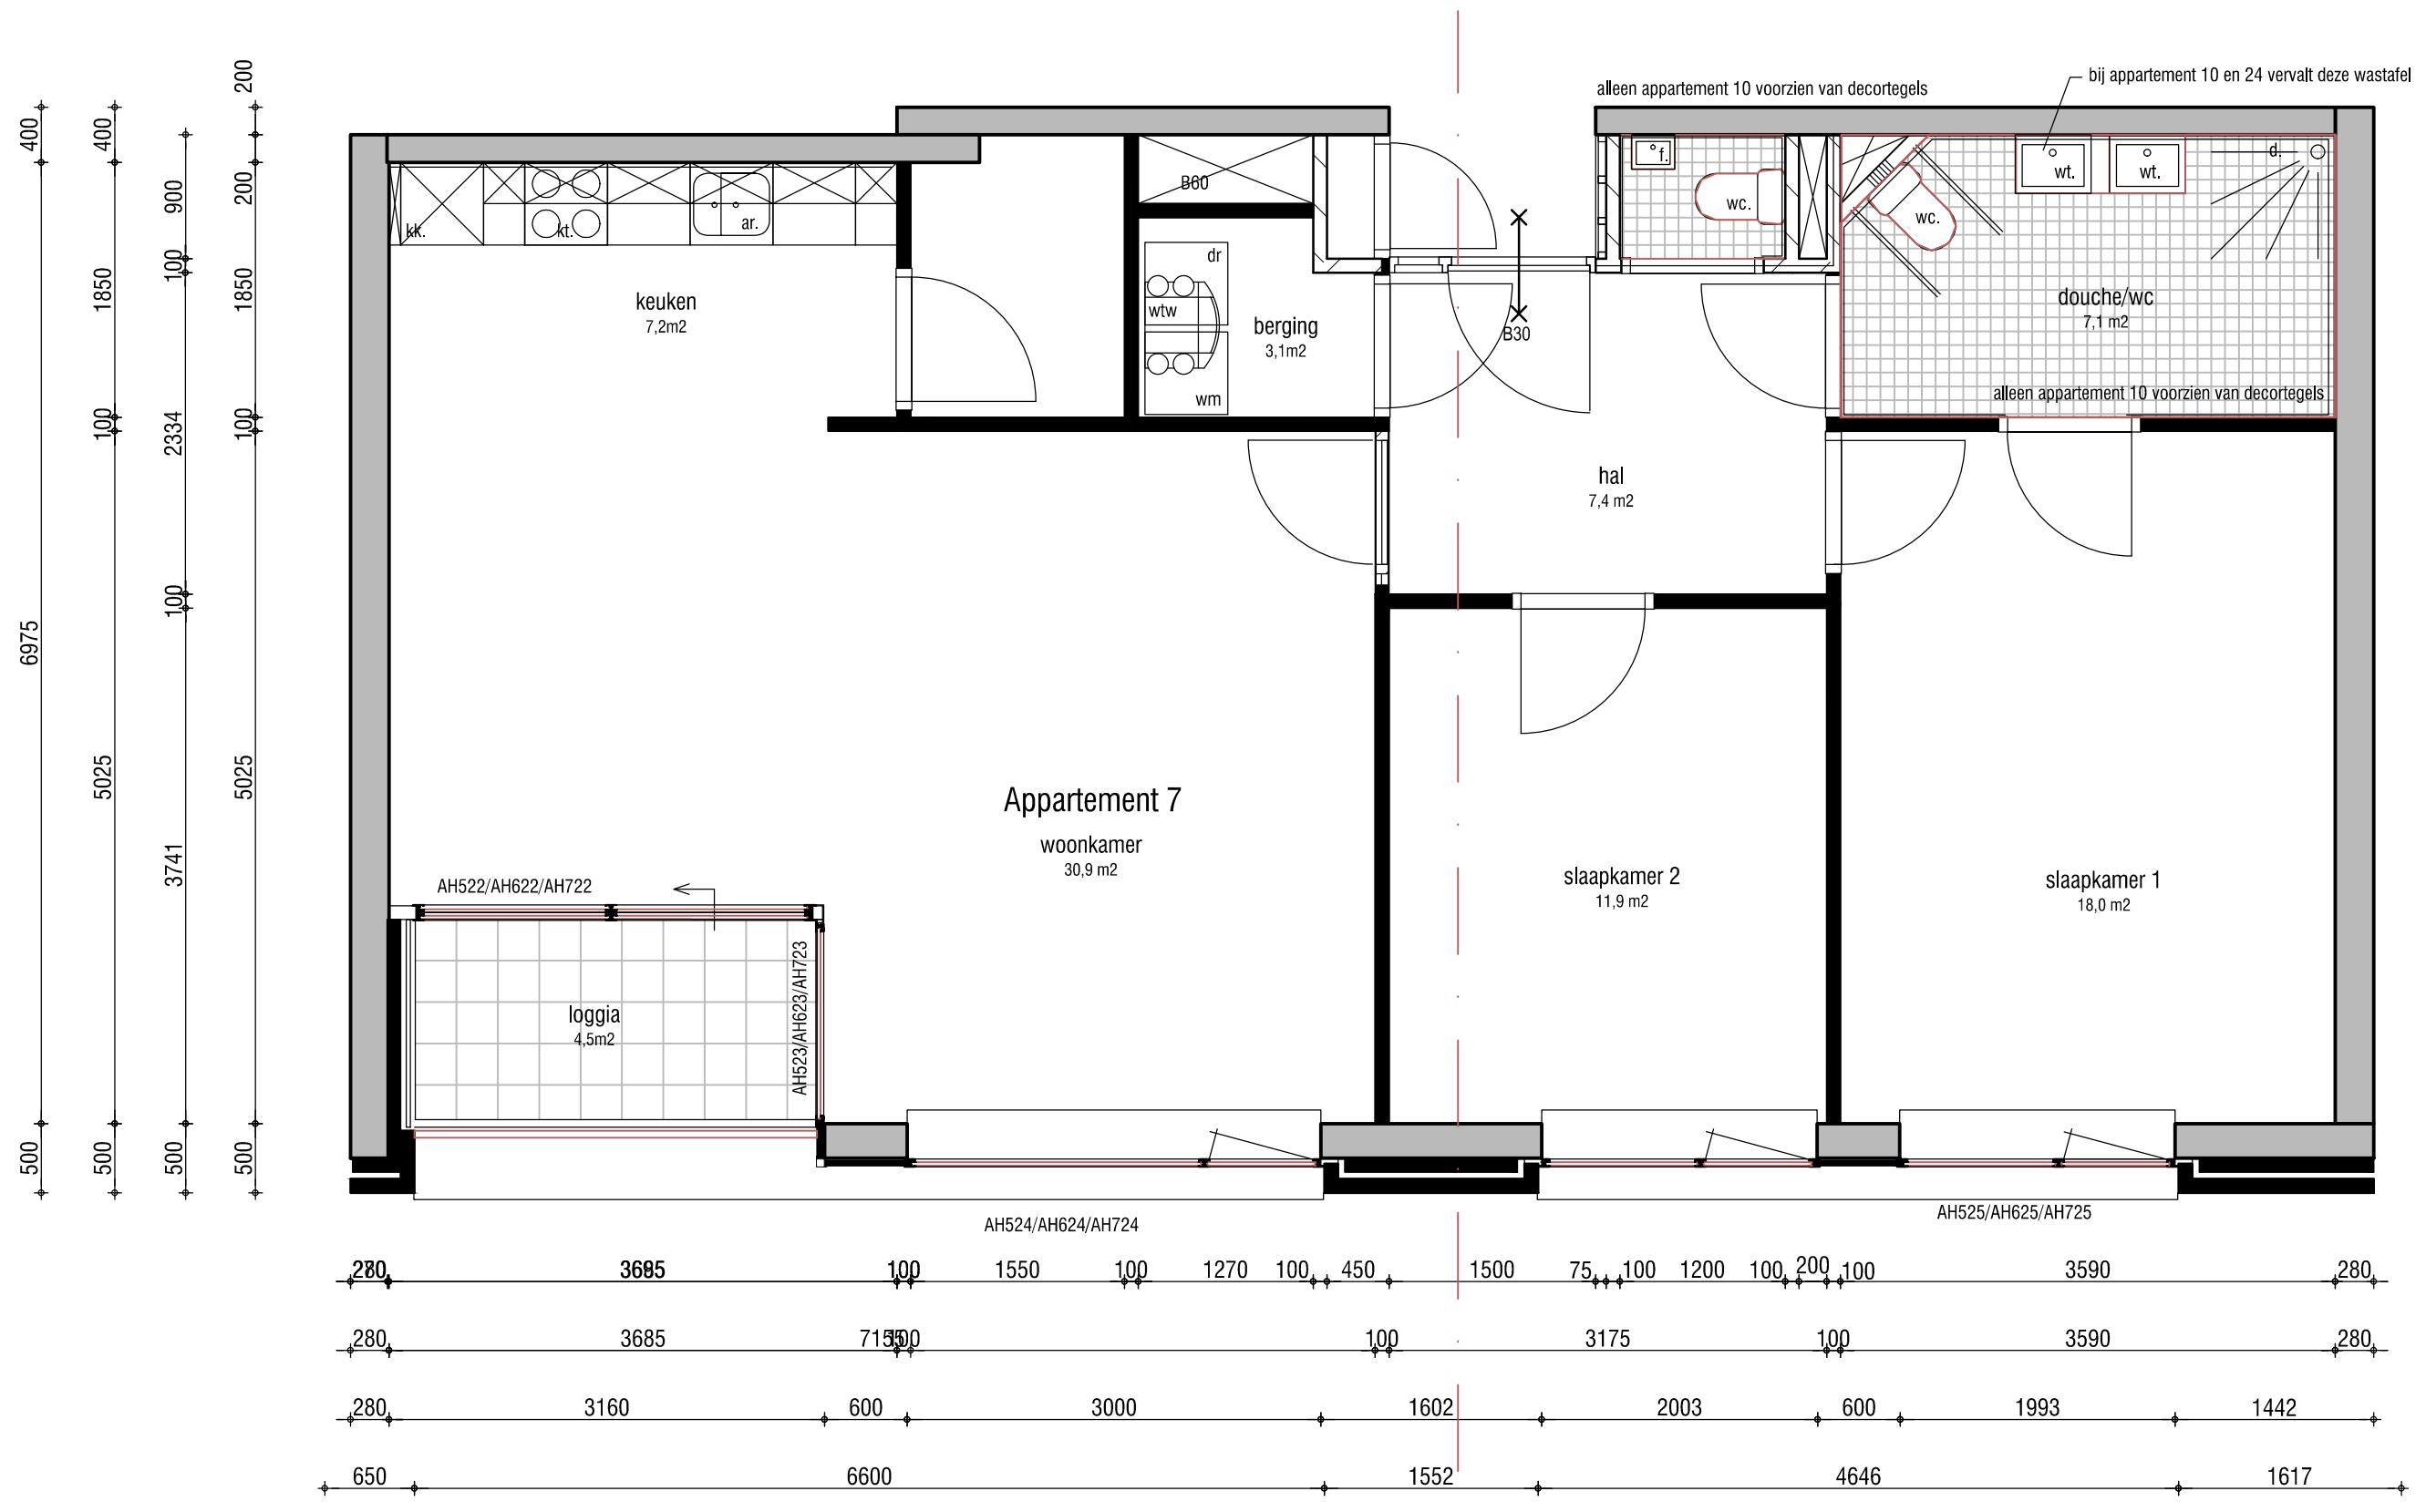

Appartement type 8 - huisnummers 8, 22, 38 en 54		Tek.no.:	20
Schaal:	1 a 50		
Formaat:	A3		
Get.:	mka		
Gew.:	dec 2006		

